



basic education

Department:
Basic Education
REPUBLIC OF SOUTH AFRICA

SENIOR CERTIFICATE EXAMINATIONS/ NATIONAL SENIOR CERTIFICATE EXAMINATIONS

ENGINEERING GRAPHICS AND DESIGN P1

2023

MARKING GUIDELINES

MARKS: 100

These marking guidelines consist of 7 pages.

ANSWERS		
1	84-0213	1
2	EXPRESS PRINTERS	1
3	PALISADE	1
4	STONE HILL	1
5	1 : 900	1
6	COMPUTER CENTRE / -BUILDING	1
7	4	1
8	ASPHALT	1
9	INSPECTION EYE	1
10	PALM TREE	1
11	GENERATOR	1
12	EAST	1
13	7500 l	2
14	100-YEAR FLOOD LINE	2
15	WATER CLOSET	1
16	BLACK	1
17	18,6	2
18	See below	3
19		3
20		4
TOTAL		30

ANSWER 18

Show ALL calculations.

ADDING OF SIDES (+, +, ...), i.e.: ✓

$$P = GD + DE + EF + FG$$

$$= (50.5 + 33.4 + 36.6 + 30.4) - (3 \times 4)$$

$$= 138.9 \text{ m}$$

✓
CONVERTED TO METERS

ANSWER 19

Show ALL calculations.

APPLYING CORRECT FORMULA, i.e.: ✓

$$A = L \times B$$


$$= [(21 \times 25) + (29 \times 7)] - (11 \times 18)$$

$$= 728 - 198$$


$$= 530 \text{ m}^2$$


ANSWER 20

20.1

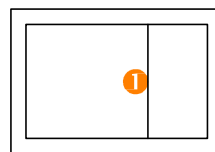OUTER RECTANGLE ✓
INNER RECTANGLE ①


20.2

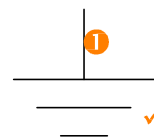① FREEHAND
FOR BOTH

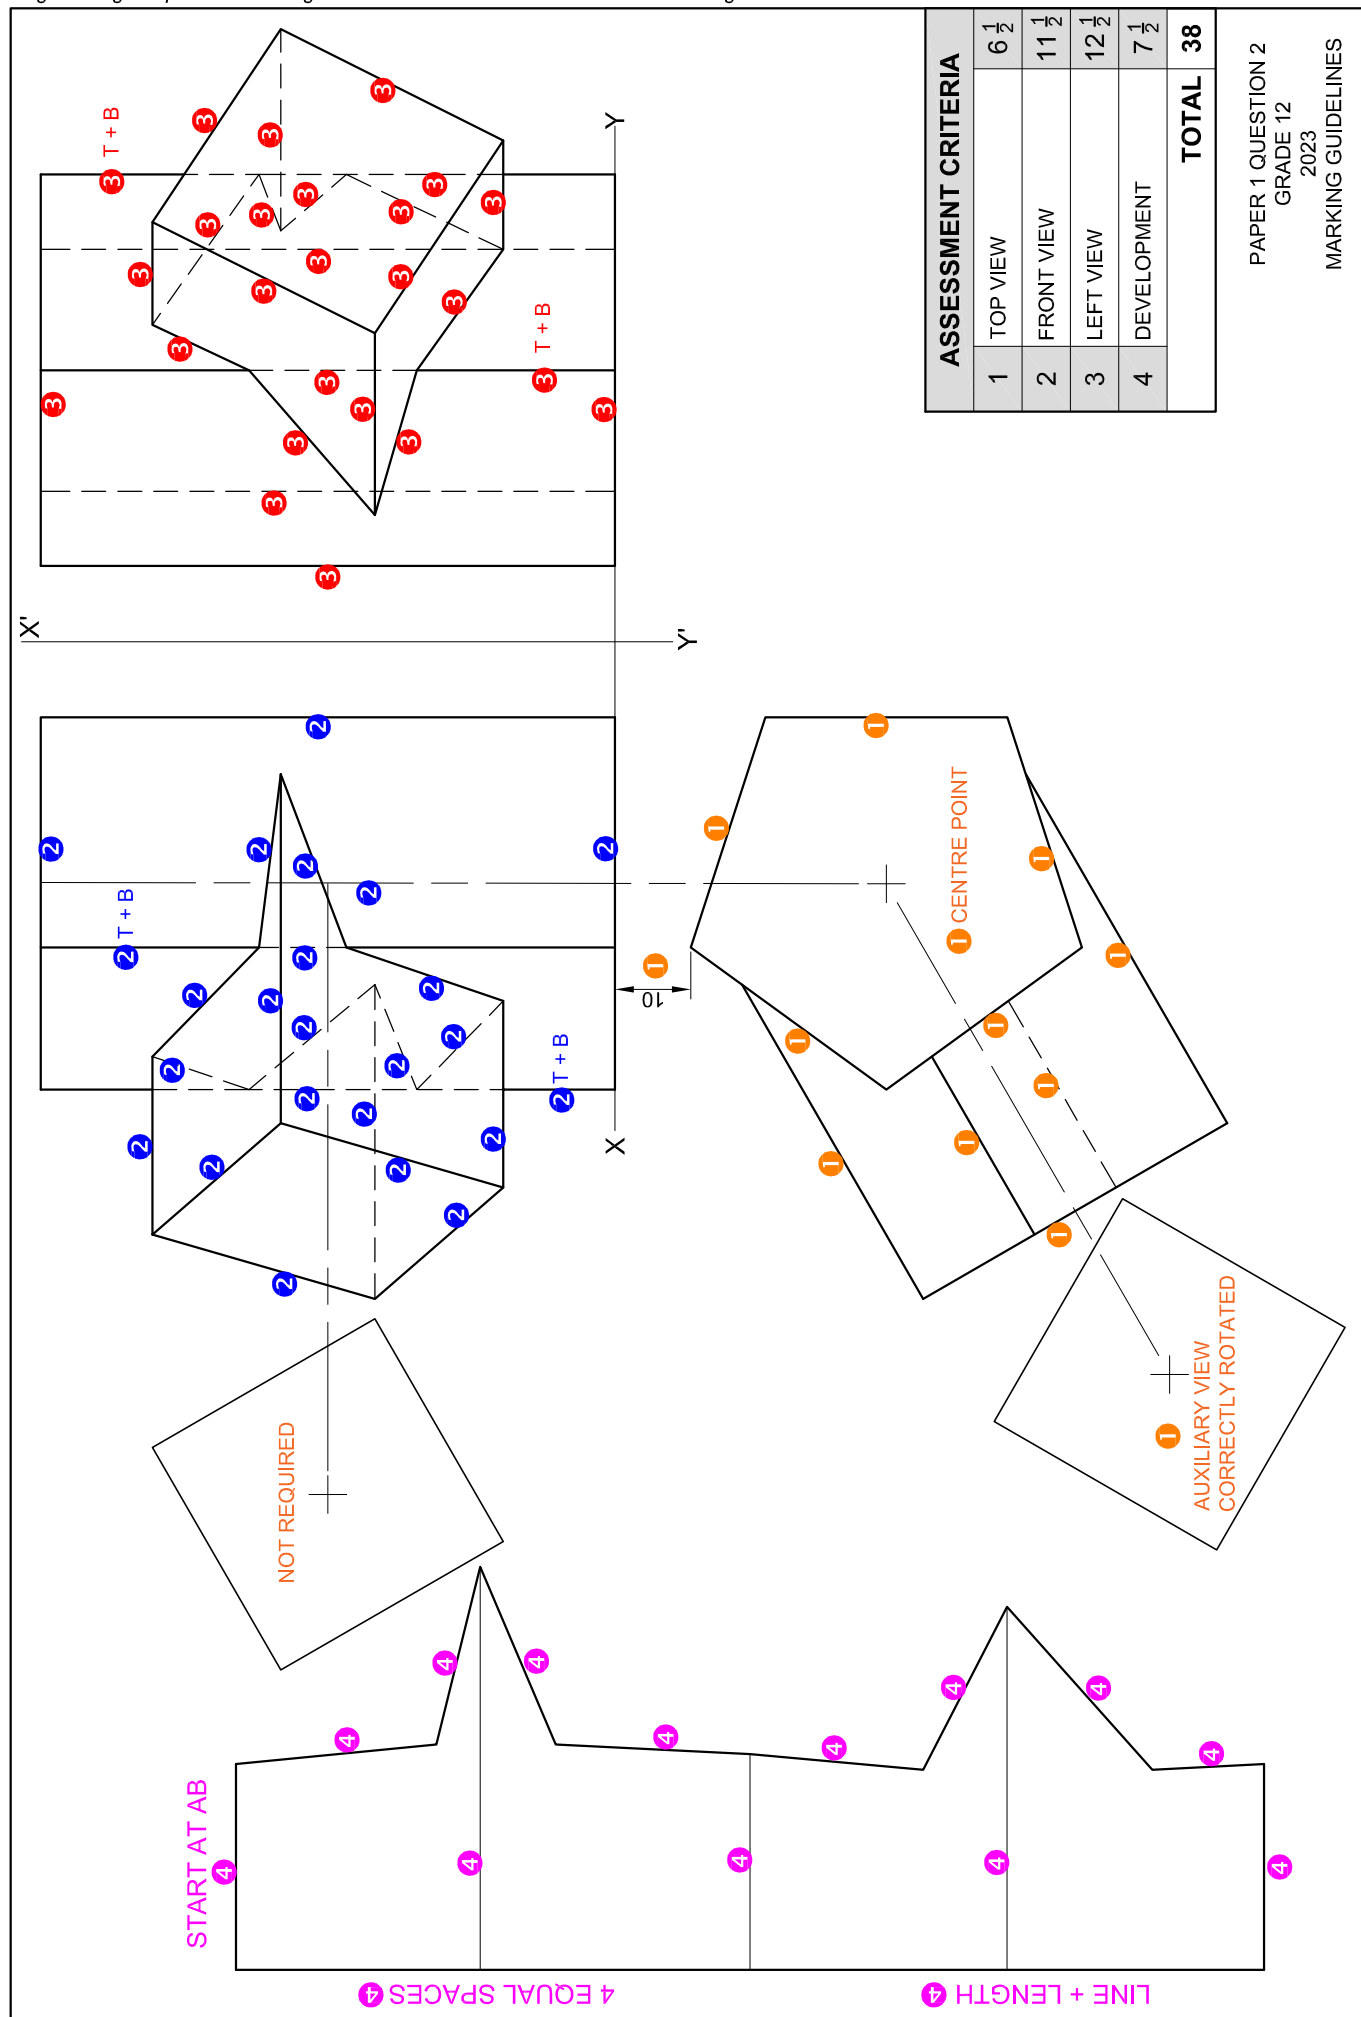


ASSESSMENT CRITERIA		
1	TOP VIEW	$6\frac{1}{2}$
2	FRONT VIEW	$11\frac{1}{2}$
3	LEFT VIEW	$12\frac{1}{2}$
4	DEVELOPMENT	$7\frac{1}{2}$
TOTAL		38

PAPER 1 QUESTION 2
GRADE 12
2023
MARKING GUIDELINES

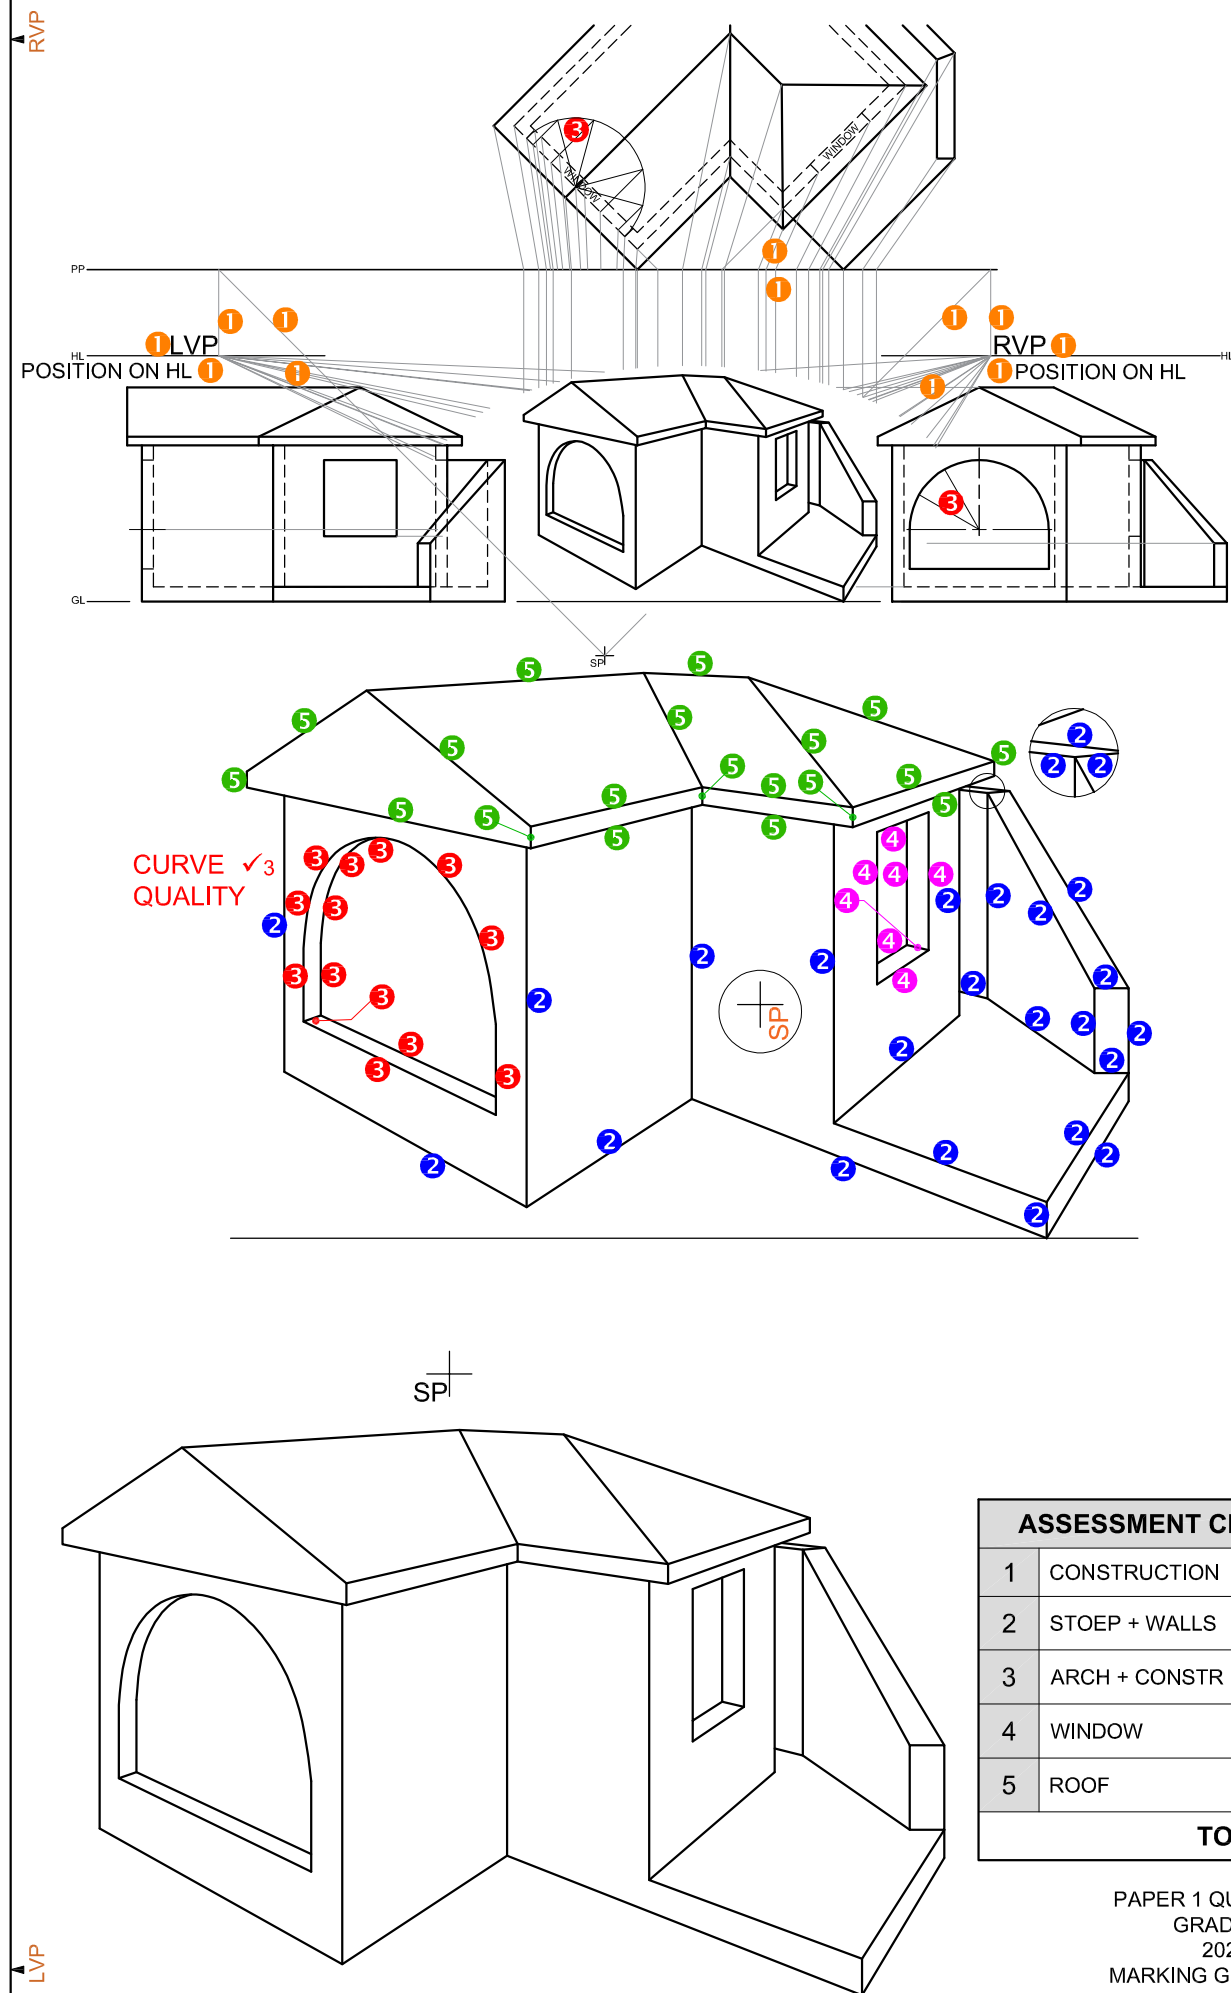

ASSESSMENT CRITERIA		
1	CONSTRUCTION	6
2	STOEP + WALLS	12 $\frac{1}{2}$
3	ARCH + CONSTR	8 $\frac{1}{2}$
4	WINDOW	3 $\frac{1}{2}$
5	ROOF	9 $\frac{1}{2}$
TOTAL		40

PAPER 1 QUESTION 3
GRADE 12
2023
MARKING GUIDELINES

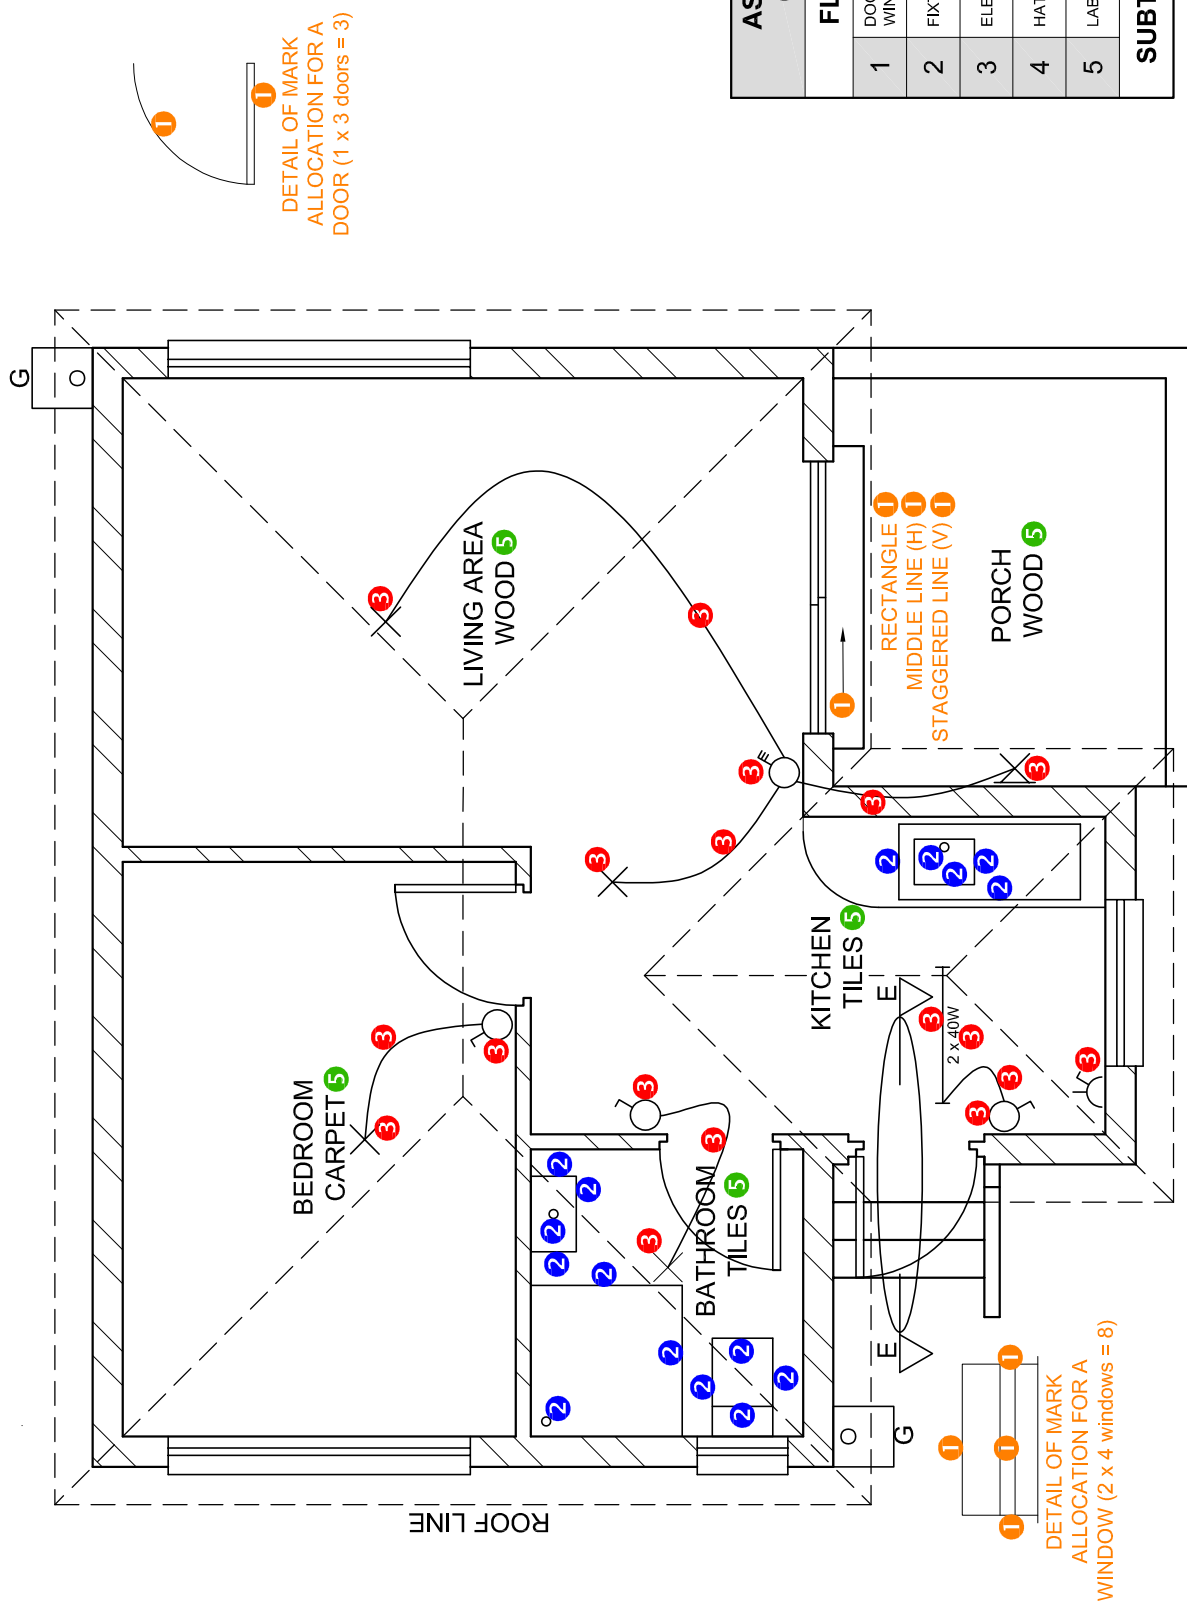


ASSESSMENT CRITERIA	
FLOOR PLAN	
1	DOORS + WINDOWS 13
2	FIXTURES 8
3	ELECTRICAL 9
4	HATCHING 3
5	LABELS $2\frac{1}{2}$
SUBTOTAL 35 $\frac{1}{2}$	

PAPER 1 QUESTION 4
GRADE 12
2023

MARKING GUIDELINES

FLOOR PLAN
SCALE 1:50

4 HATCHING ALLOCATION	
1 SANS COMPLIANT (TYPE)	
2 HATCHING CORRECTLY APPLIED	
3 TOTAL	

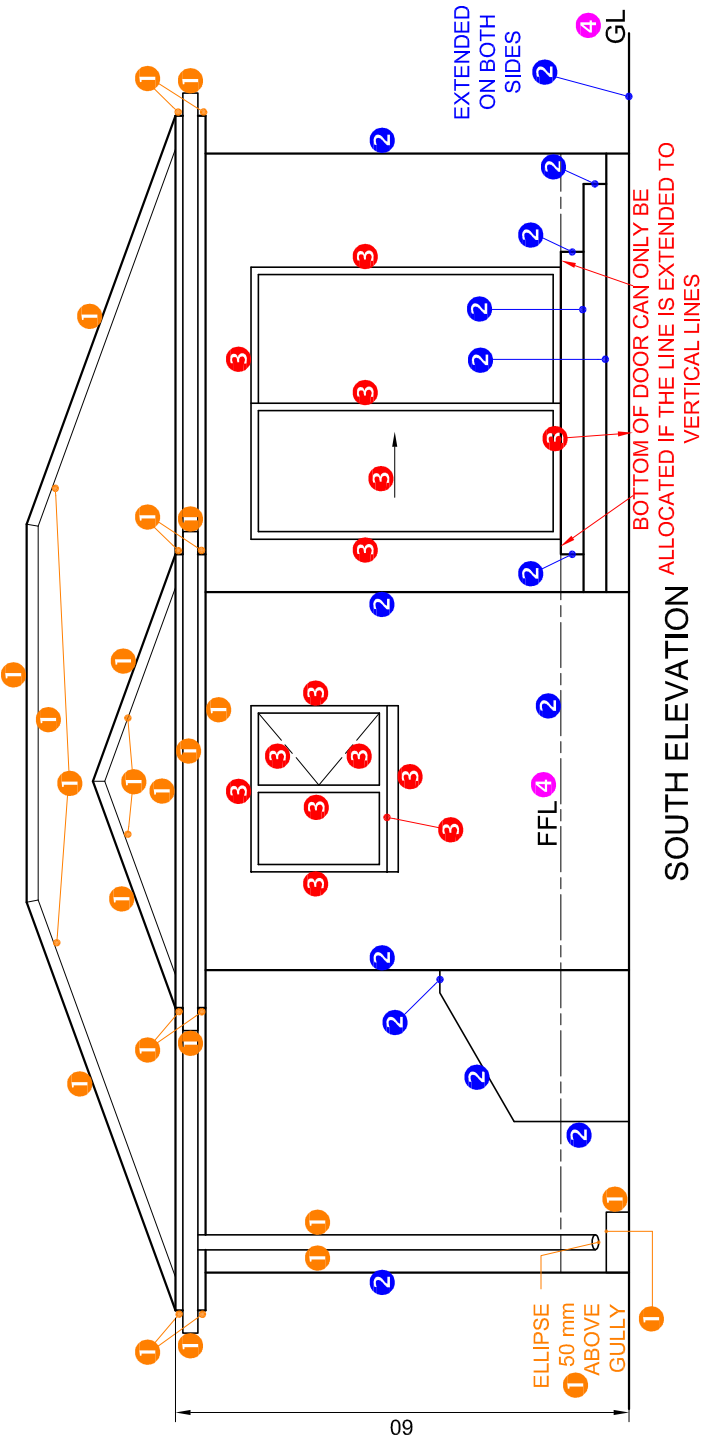

ASSESSMENT CRITERIA	
SOUTH ELEVATION	
1	ROOF + RWDP + GULLY
2	WALLS + FFL
3	DOOR + WINDOW
4	LABELS
SUBTOTAL	
27	

PAPER 1 QUESTION 4
GRADE 12
2023
MARKING GUIDELINES

3. HATCHING ALLOCATION

SANS COMPLIANT



0.5

HATCHING CORRECTLY APPLIED


0.5

TOTAL

1

1. MARK ALLOCATION FOR ROOF

A: ROOF ANGLE	1
B: ROOF SHEET	1
C: PURLIN + SPACING	1,5
D: TRUSS + OVERHANG	3
E: FACIA	1,5
F: GUTTER	1
G: WALL PLATE	1
H: BRANDERING + SPACING	1
J: CEILING BOARD	0,5
TOTAL	11,5

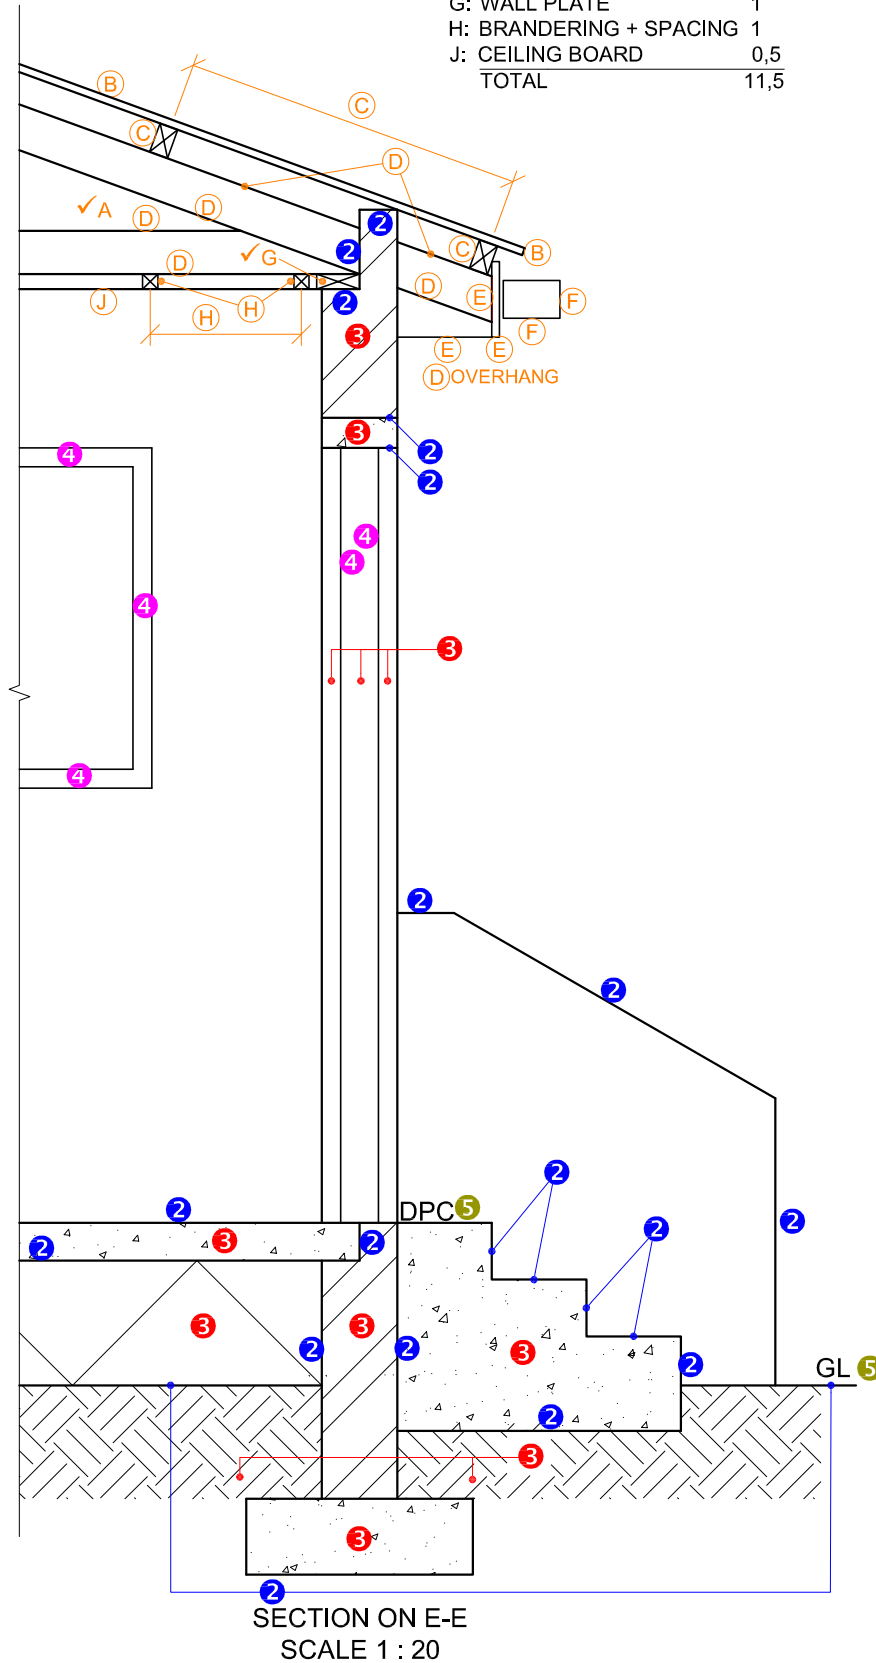**ASSESSMENT CRITERIA****DETAILED SECTION**

1	ROOF DETAIL	11 $\frac{1}{2}$
2	SLAB + WALL + STEP	9
3	HATCHING	5 $\frac{1}{2}$
4	WINDOW + DOOR	2 $\frac{1}{2}$
5	LABELS	1
SUBTOTAL		29 $\frac{1}{2}$

PAPER 1 QUESTION 4
GRADE 12
2023
MARKING GUIDELINES