higher education & training

Department:
Higher Education and Training
REPUBLIC OF SOUTH AFRICA

MARKING GUIDELINE

NATIONAL CERTIFICATE


BUILDING AND STRUCTURAL CONSTRUCTION N4

28 NOVEMBER 2019

This marking guideline consists of 9 pages.


Copyright reserved

QUESTION 1

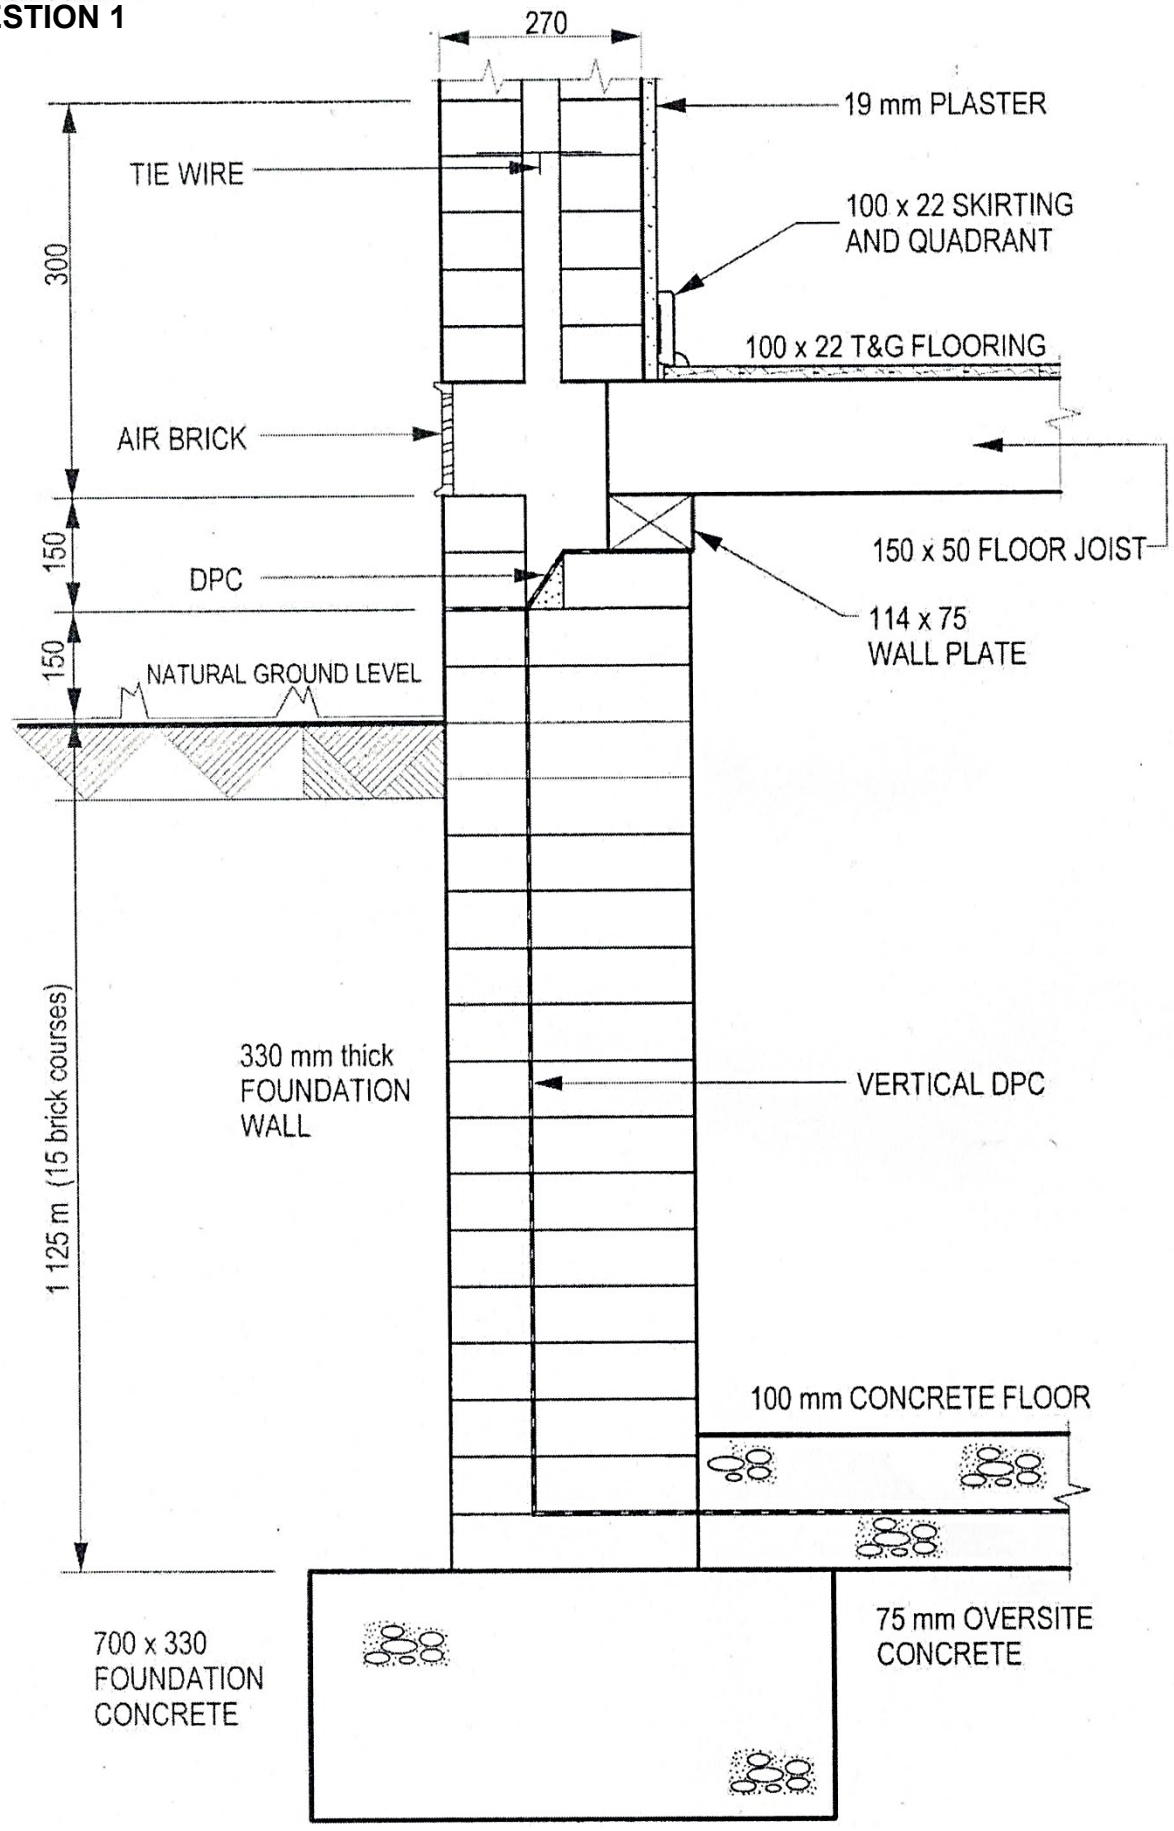


VERTICAL SECTION THROUGH AN EXTERNAL BASEMENT WALL
SCALE 1:10 **[24]**

QUESTION 2

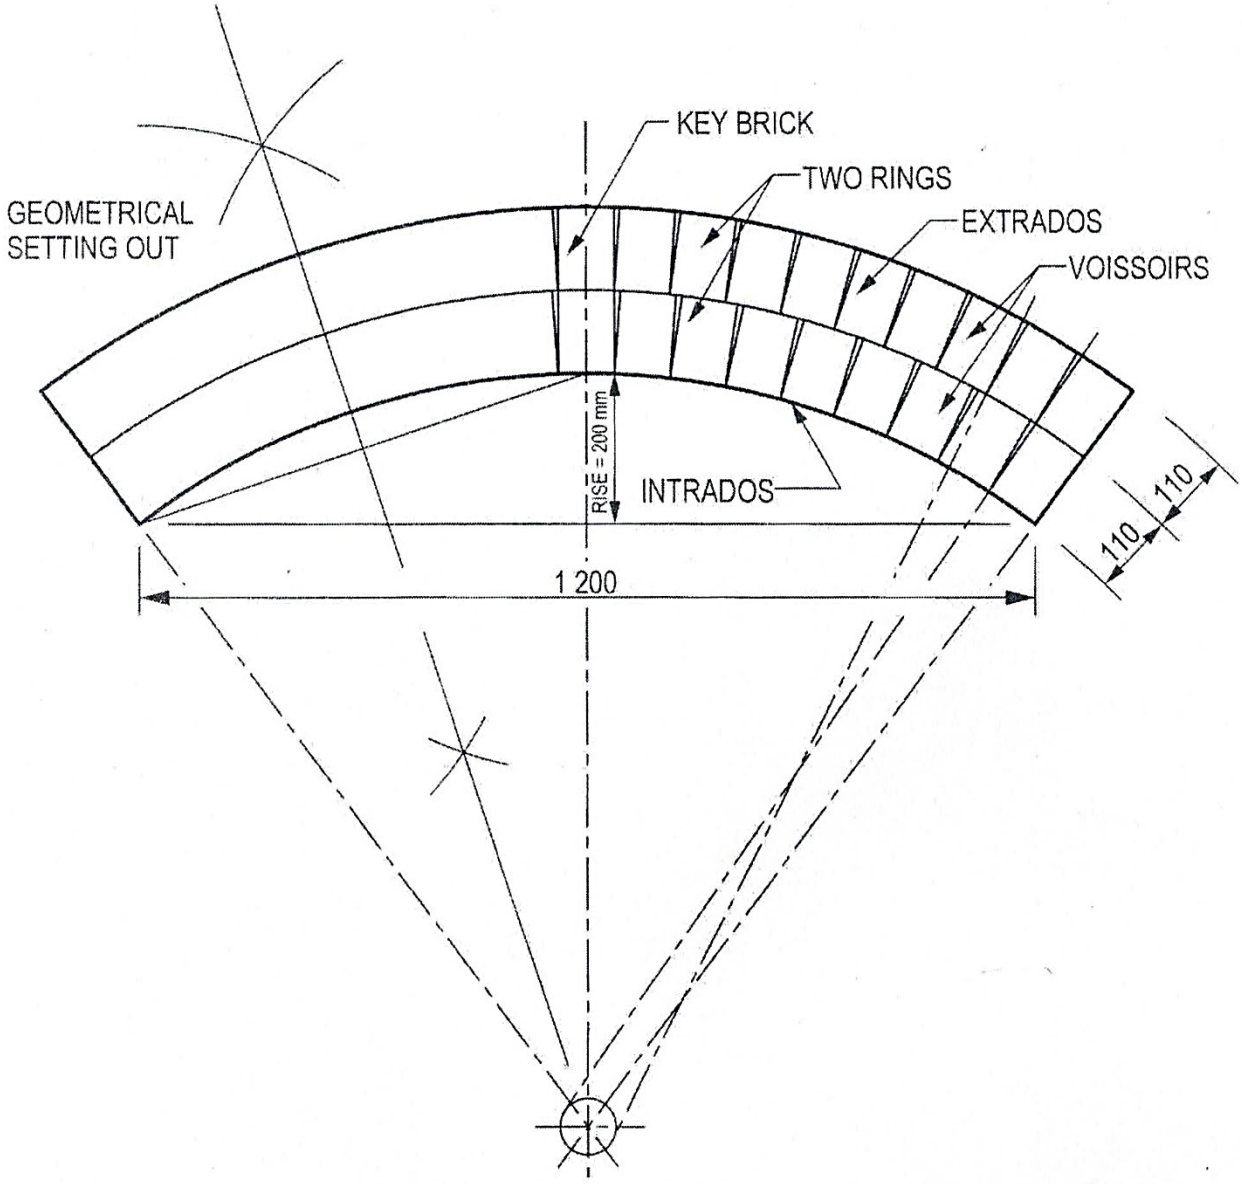


TWO-RING ROUGH-BRICK SEGMENTAL ARCH
SCALE 1:10 **[12]**

QUESTION 3

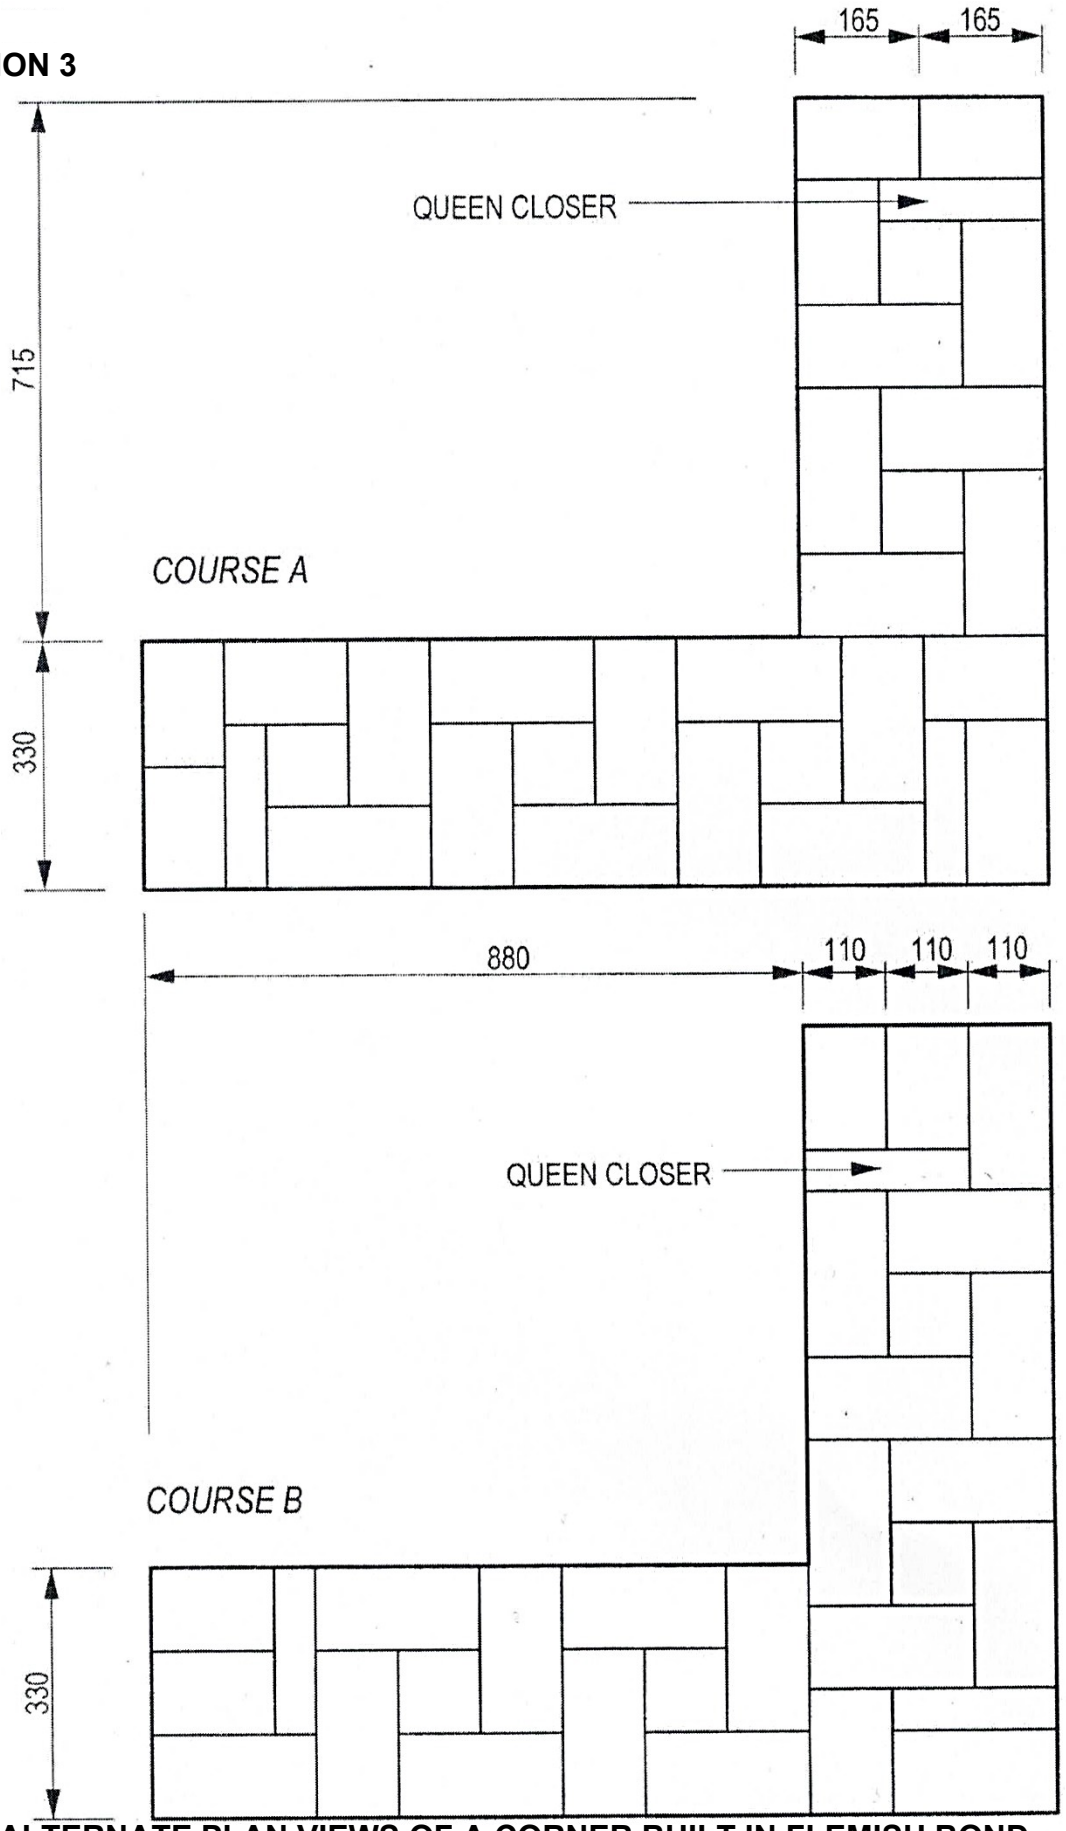


ALTERNATE PLAN VIEWS OF A CORNER BUILT IN FLEMISH BOND
SCALE 1:10 **[10]**

QUESTION 4

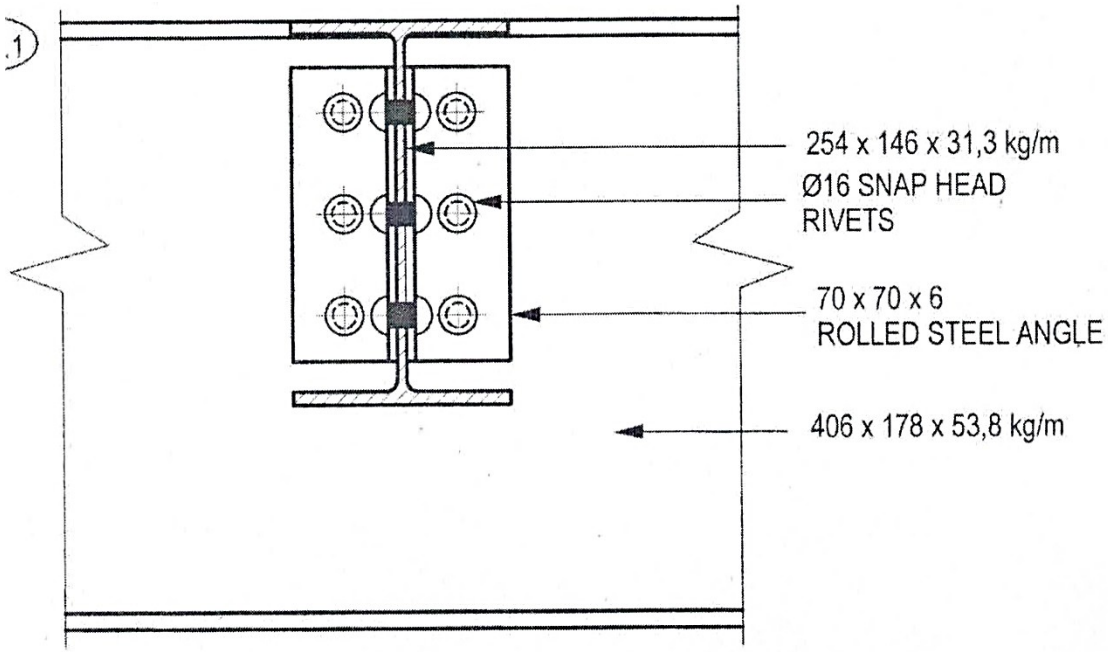


VERTICAL SECTION THROUGH THE SECONDARY BEAM
SCALE 1:5

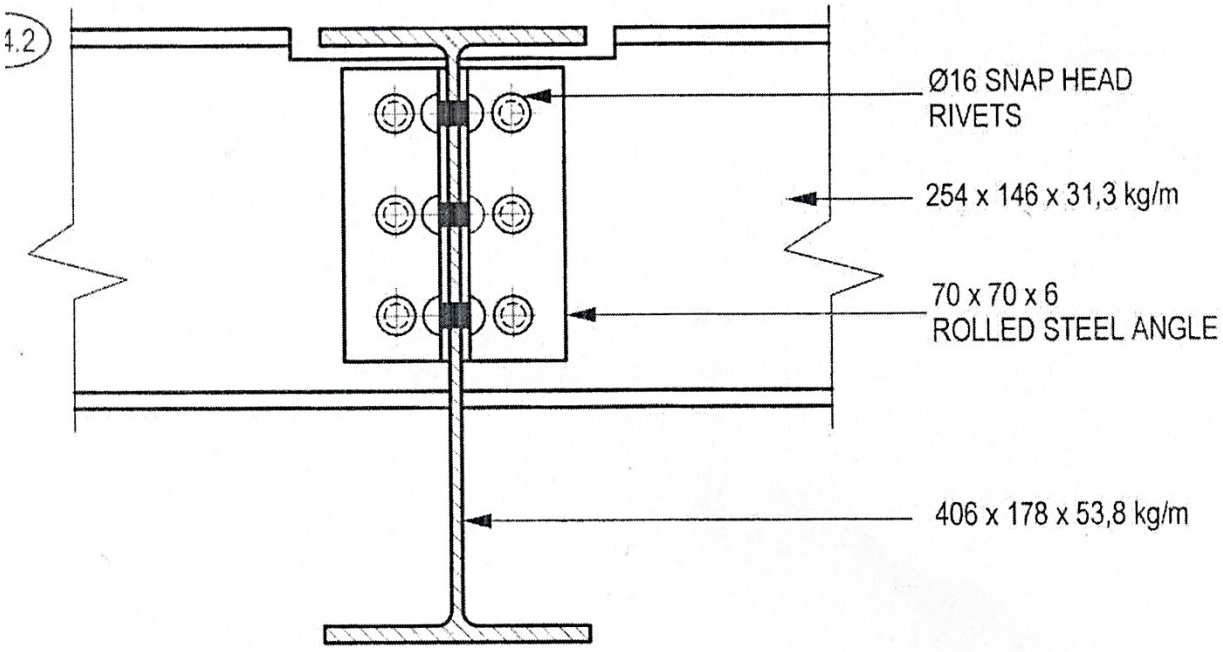


VERTICAL SECTION THROUGH THE MAIN BEAM
SCALE 1:5 **[21]**

QUESTION 5

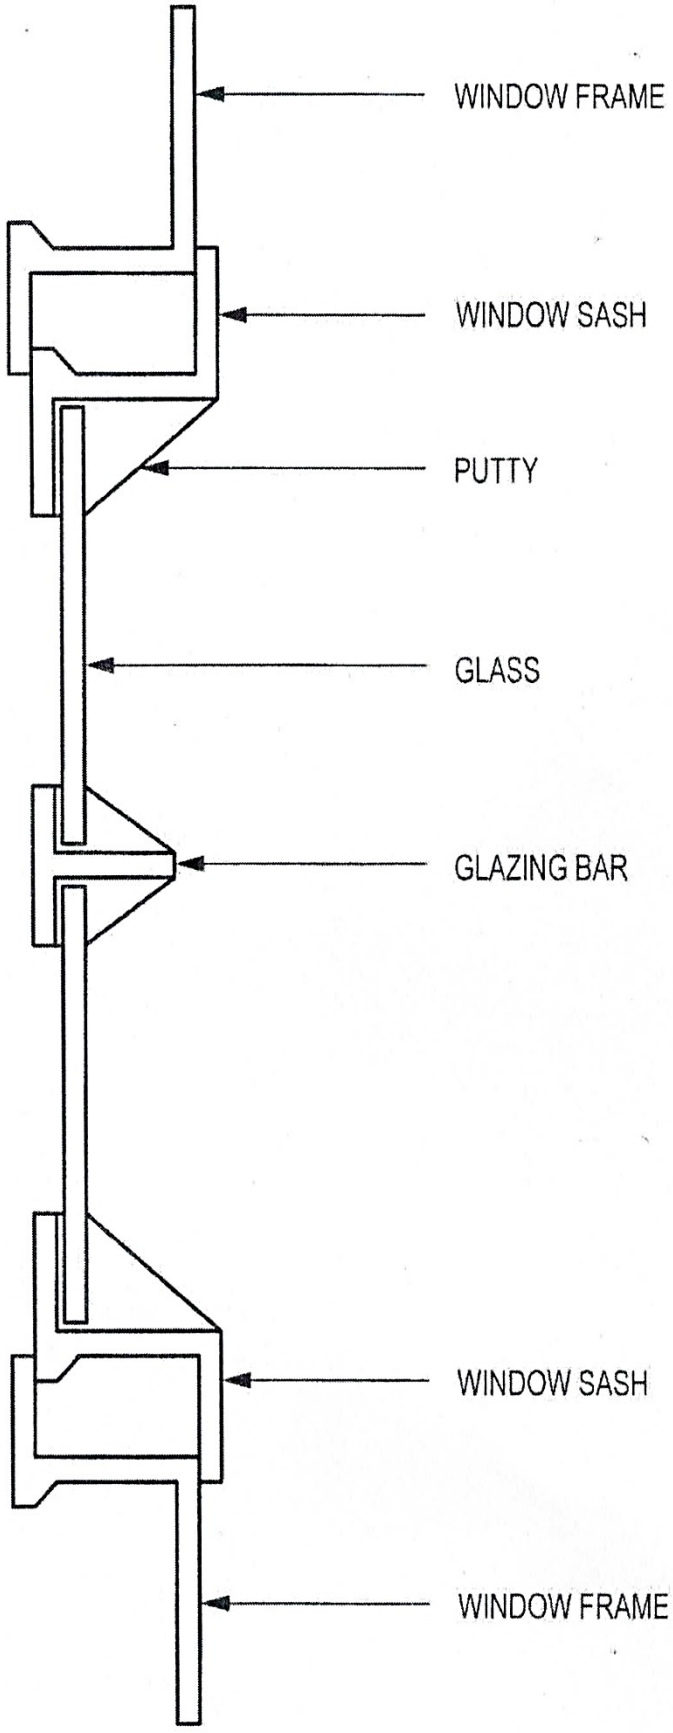

VERTICAL SECTION THROUGH A STEEL WINDOW FRAME
SCALE 1:2 **[10]**

QUESTION 6

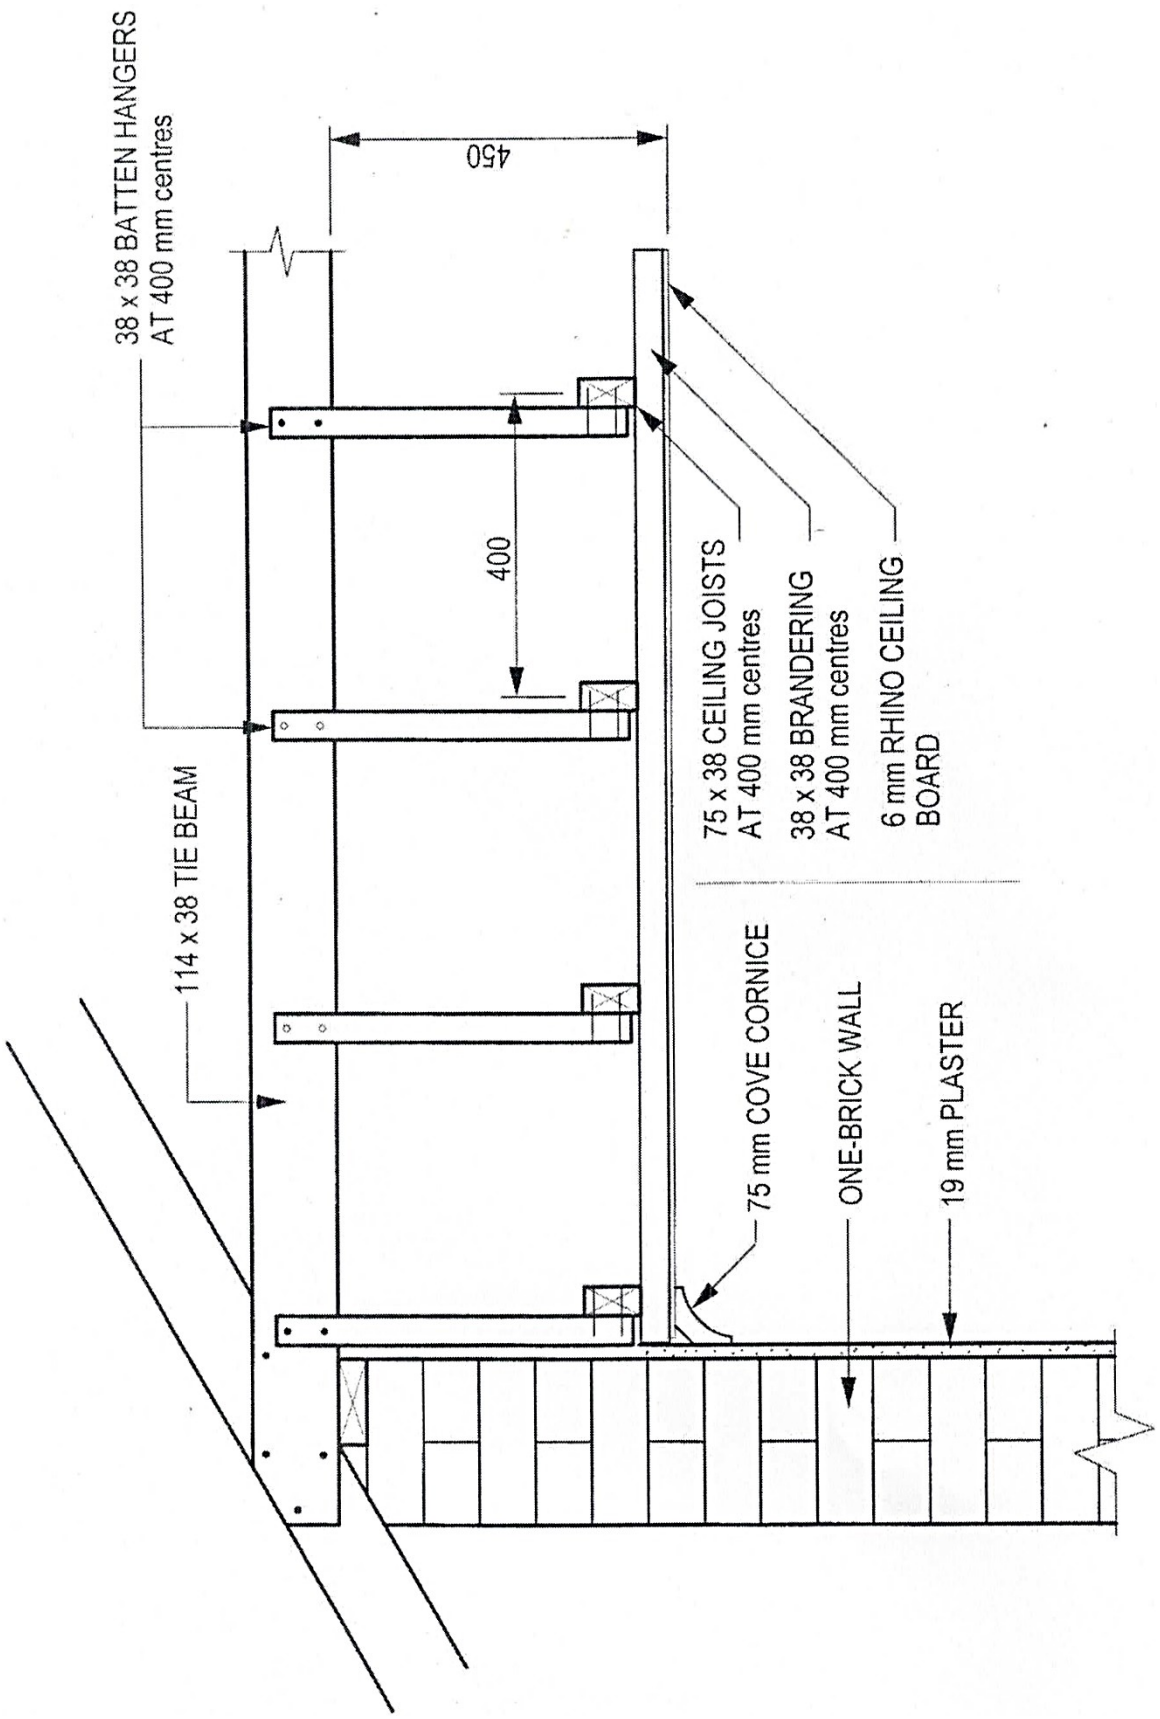

SECTIONAL FRONT VIEW OF A SUSPENDED CEILING
SCALE 1:10

[15]

QUESTION 7

- Mark out the position of the window frame on the wall.
- Place two bricks, on edge, on top of the wall 100 mm inside the marked positions of the window.
- Place the window on top of the bricks.
- Drive a nail halfway into the top of two timber stays then hook the stay onto the top of the window frame to hold the frame in position.
- Place the frame on the marked positions on the wall.
- Place a sole plate on the inside concrete floor and weigh down with bricks or concrete blocks to keep the stays in position.
- Proceed with levelling the frame using folding wedges on top of the bricks-on-edge and plumbing the frame by moving the stays forward or backwards.
- The window is now ready to be built in.

NOTE: The sequence of steps must be in the correct order for 8 marks. Allow only marks up till where the correct order stops. **[8]**

MARK SHEET

QUESTION 1		
MARK ALLOCATION		
Correctness:		16
Conc Fndt	1	
Heights corr.	3	
Foundation wall	1	
Cavity wall	1	
Concrete floor	2	
Floor joist	2	
Flooring	1	
Skirting&Quadrant	2	
All DPC corr	2	
Ground Level	1	
Accuracy		3
Dimensions		2
Labels		3
Total		24

QUESTION 2		
MARK ALLOCATION		
Correctness:		8
Span & Rise corr.	1	
Geo set-out corr.	1	
2 Rings	2	
Bricks corr.	2	
V-joints	2	
Accuracy		2
Labels		1
Dimensions		1
Total		12

QUESTION 3		
MARK ALLOCATION		
Correctness:		6
Wall width corr	1	
Corr bonding	3	
Stopped ends	2	
Accuracy		2
Dimensions		1
Labels		1
Total		10

QUESTION 4			
MARK ALLOCATION		MARK ALLOCATION	
Correctness: (Q4.1)		Correctness: (Q4.2)	
Correct view	1	Correct view	1
Main beam	1	Main beam	1
Secondary beam	1	Secondary beam	1
Angles	2	Angles	2
Rivets	2	Rivets	2
Total	7	Total	7

MARK ALLOCATION	
Accuracy	3
Notch in place	1
Lables	2
Titles	1
Total	7

SUMMARY
7 + 7 + 7
Total = 21 Marks

QUESTION 5		
MARK ALLOCATION		
Correctness:		6
Vertical view Corr.	1	
Frame head.	2	
Sash	2	
Glazing bar	1	
Accuracy		2
Labels		2
Total		10

QUESTION 6		
MARK ALLOCATION		
Correctness:		10
Rafter & Tie beam	1	
Wall & wall plate	1	
Batten hangers	2	
Ceiling joist	2	
Ceiling	2	
Plaster & Cornice	2	
Accuracy		3
Labels		2
Total		15

QUESTION 7
REFER TO MARKING GUIDELINE
TOTAL = 8

TOTAL: 100

Copyright reserved