



basic education

Department:
Basic Education
REPUBLIC OF SOUTH AFRICA

NATIONAL SENIOR CERTIFICATE

GRADE 12

ENGINEERING GRAPHICS AND DESIGN P1

NOVEMBER 2025

MARKING GUIDELINES

MARKS: 100

These marking guidelines consist of 7 pages.

ANSWERS		
1	1 : 400	1
2	02/07/2025	1
3	58	1
4	STRAND	1
5	8/ EIGHT	1
6	6000	1
7	<u>DIRECTION OF GATE OPENING</u>	1
8	1 : 40	1
9	1/ ONE	1
10	MANHOLE	1
11	DRIVEWAY	1
12	<u>ELECTRIC FENCE</u>	1
13	CONC	1
14	BLUE	1
15	DRAINAGE PLANS	1
16	3/ THREE	2
17	26500 ✓ ANSWER IN MILLIMETRES✓	2
18	See below	3
19		3
20		5
TOTAL		30

ANSWER 18

Show ALL calculations.

APPLYING CORRECT FORMULA ✓
 LENGTH OF FENCE
 $= (AB + BC + DE + EA) - \text{GATE}$
 $= (46,07 + 38,84 + 30 + 64,78) - 6$
 $= 173,69$ ✓ ANSWER IN METRES ✓


ANSWER 19

Show ALL calculations.

APPLYING CORRECT FORMULA ✓
 $5,5 \times 8 = 44$
 $3,5 \times 5 = 17,5$
 $8 \times 12 = 96$
 $7 \times 5 = 35$ ✓
 $= 192,5 \text{ m}^2$ ✓ ANSWER IN SQUARE METRES, WITH m^2 INCL.

ANSWER 20

(a) RAMP

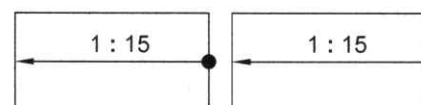

RECTANGLE 0.5
 ARROW + DOT + DIRECTION 0.5 + 0.5 + 0.5
 GRADIENT 0.5
 FREEHAND 0.5

(b) DOUBLE SINK





TOP LINE/ RECTANGLE 0.5
 BOTTOM RECTANGLE(S) 0.5
 TWO BOWLS 1


PAPER 1 QUESTION 2
GRADE 12
November 2025
MARKING GUIDELINES

✓1
PENTAGON CORRECTLY DRAWN/
ACCEPTABLE CONSTRUCTION



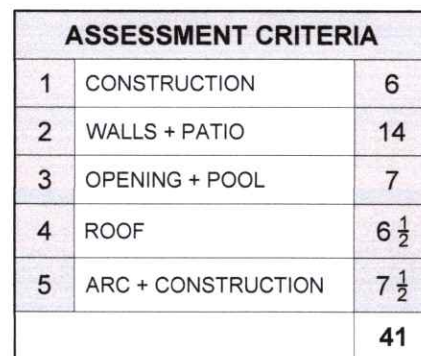

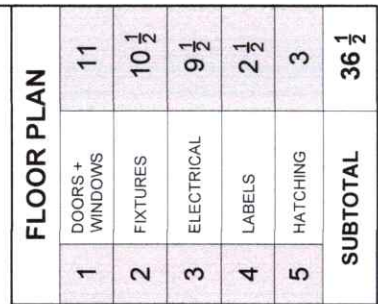

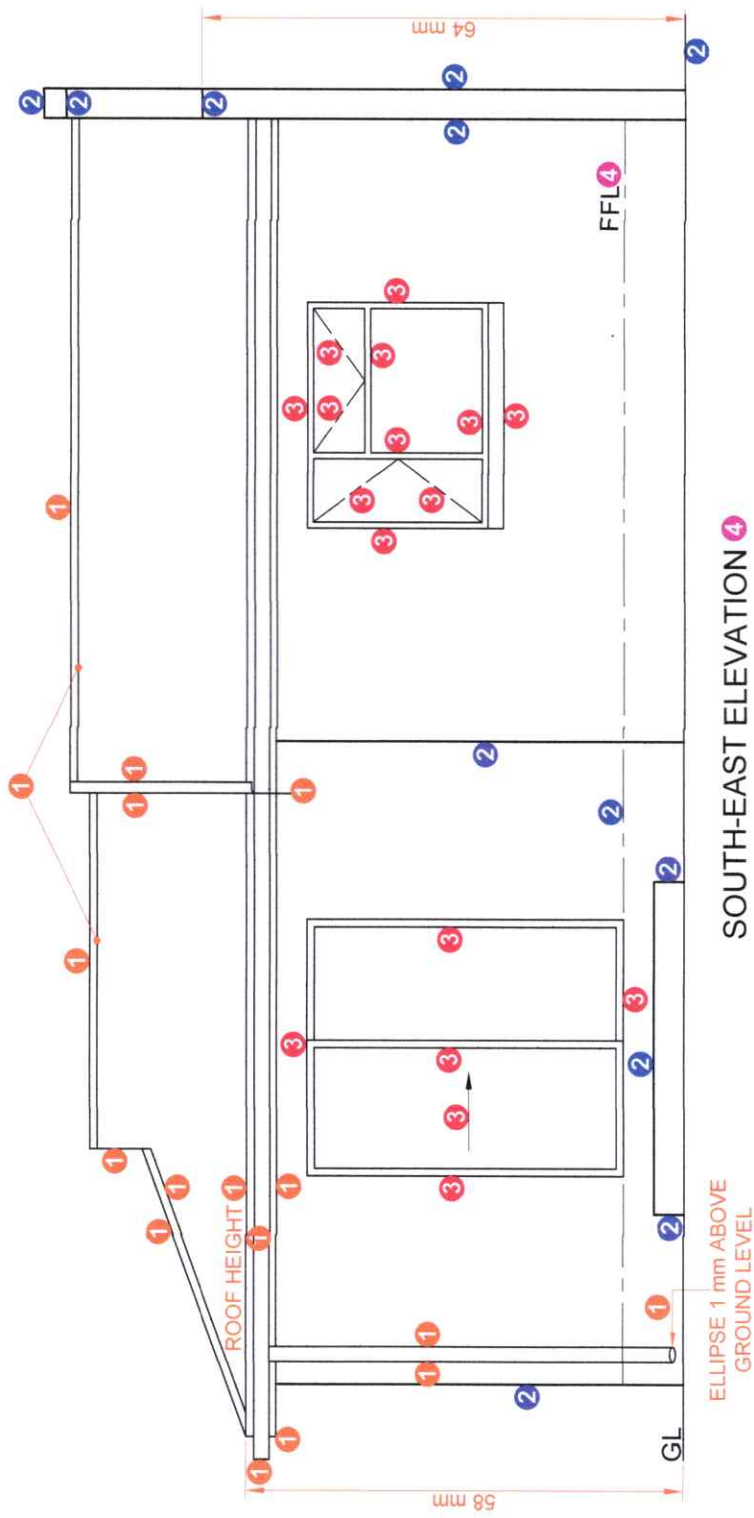


SOUTH-EAST ELEVATION		
1	ROOF + RWDP	8 ¹ / ₂
2	WALLS + STEPS	6
3	DOOR + WINDOW	8 ¹ / ₂
4	LABELS	1
SUBTOTAL		24

1. MARK ALLOCATION FOR ROOF

A: ROOF ANGLE	1
B: ROOF SHEET	1
C: PURLIN + SPACING	1,5
D: TRUSS + OVERHANG	3
E: WALL PLATE	1
F: FASCIA	1
G: GUTTER	1
H: BARGE BOARDS	1,5
J: BRANDING + SPACING	1
K: CEILING BOARD	0,5
TOTAL	12,5

HATCHING ALLOCATION

SANS COMPLIANT (TYPE)	0.5
HATCHING CORRECTLY APPLIED	0.5
TOTAL	1

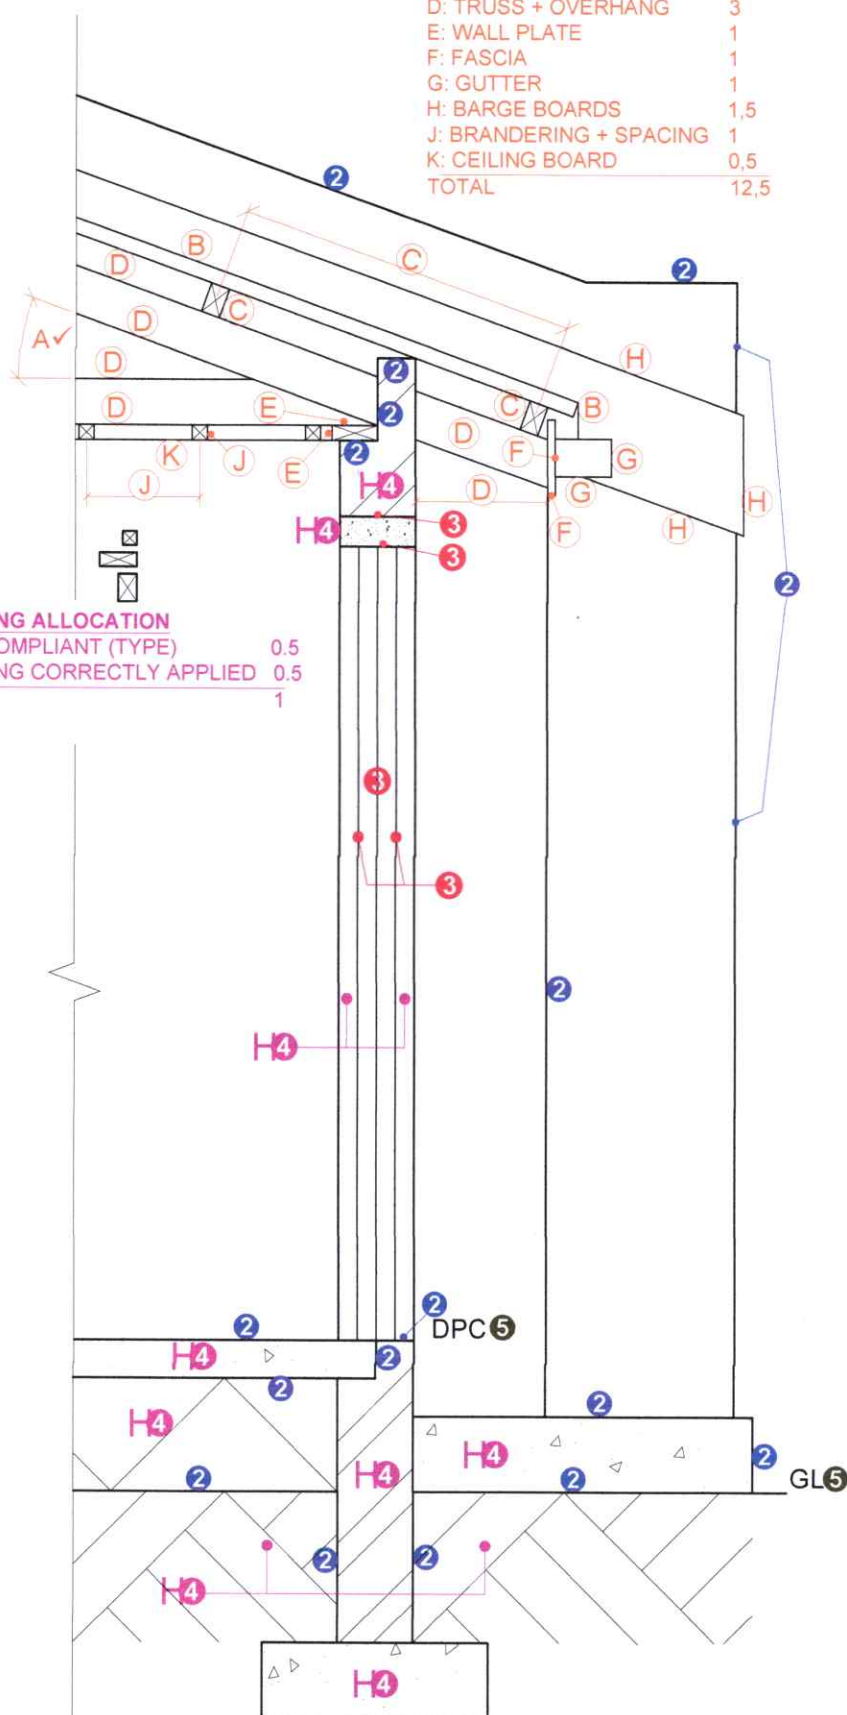


SECTION A-A
SCALE 1 : 20

DETAILED SECTION

1	ROOF DETAIL	12 $\frac{1}{2}$
2	SLAB + WALLS + STEP	8 $\frac{1}{2}$
3	DOOR + LINTEL	2
4	HATCHING	5 $\frac{1}{2}$
5	LABELS	1
SUBTOTAL		29 $\frac{1}{2}$

PAPER 1 QUESTION 4
GRADE 12
November 2025
MARKING GUIDELINES

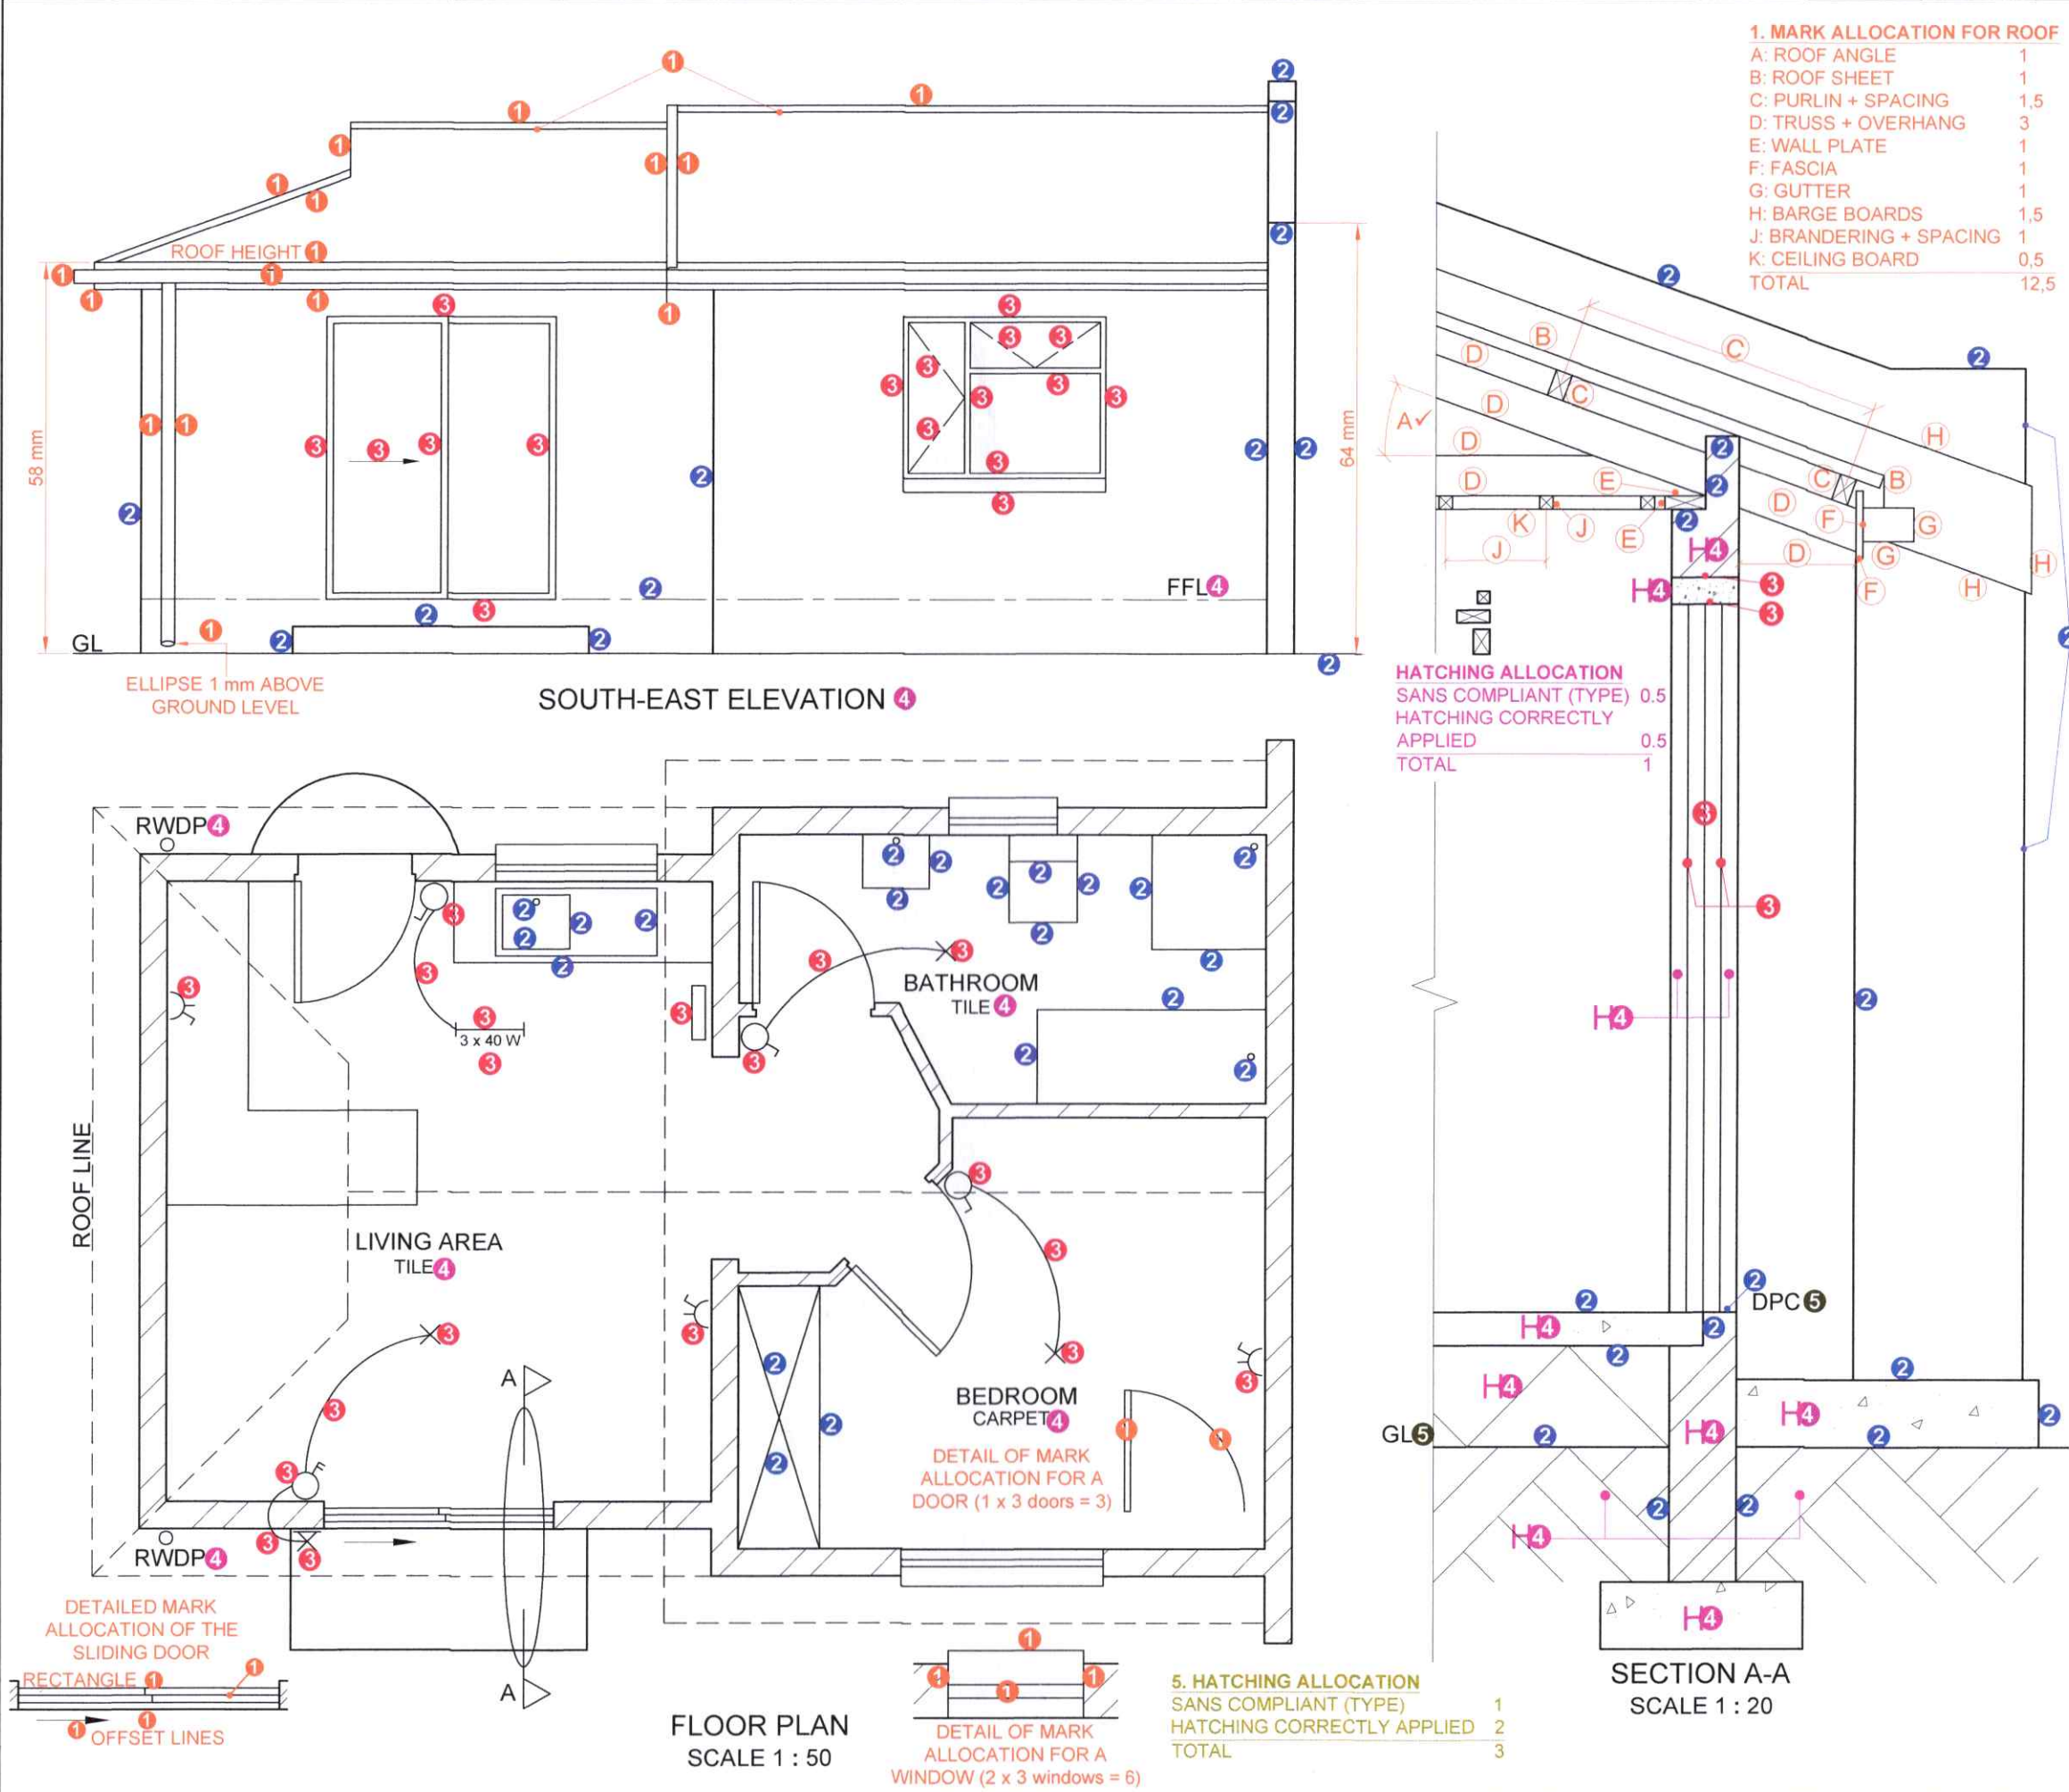

MARK ALLOCATION FOR SECTION OF ROOF		FOR OFFICIAL USE ONLY			
A		INCORRECT SCALE(S) USED			
B		NON-ALIGNMENT OF VIEWS			
C		VIEW(S) ROTATED			
D		SECTION VIEWED INCORRECTLY			
E		INCORRECT LETTERING			
F					
G					
H					
J					
K					
TOTAL				TOTAL	

ASSESSMENT CRITERIA					
FLOOR PLAN					
		POSSIBLE	OBTAINED	SIGN	MODERATED
1	DOORS + WINDOWS	11			
2	FIXTURES	10 1/2			
3	ELECTRICAL	9 1/2			
4	LABELS	2 1/2			
5	HATCHING	3			
SUBTOTAL		36 1/2			
SOUTH-EAST ELEVATION					
1	ROOF + RWDP	8 1/2			
2	WALLS + STEPS	6			
3	DOOR + WINDOW	8 1/2			
4	LABELS	1			
SUBTOTAL		24			
DETAILED SECTION					
1	ROOF DETAIL	12 1/2			
2	SLAB + WALLS + STEP	8 1/2			
3	DOOR + LINTEL	2			
4	HATCHING	5 1/2			
5	LABELS	1			
SUBTOTAL		29 1/2			
TOTAL		90			
PENALTIES (-)					
GRAND TOTAL					