



basic education

Department:
Basic Education
REPUBLIC OF SOUTH AFRICA

SENIOR CERTIFICATE EXAMINATIONS/ NATIONAL SENIOR CERTIFICATE EXAMINATIONS

ENGINEERING GRAPHICS AND DESIGN P1

MAY/JUNE 2026

MARKING GUIDELINES

MARKS: 100

These marking guidelines consist of 7 pages.

ANSWERS		
1	1 : 1000	1
2	GOUTA	1
3	E MOKOENA	1
4	VERIFY ALL DIMENSIONS AND/OR LEVELS	1
5	PALM GROVE	1
6	9 / NINE	1
7	2500	1
8	ELECTRICITY METER / WATT METER	1
9	200	1
10	INSPECTION EYE	1
11	SHRUBS	1
12	6 / SIX	1
13	B	1
14	BRICK PAVING	1
15	INSPECTION CHAMBER	2
16	NEW CONCRETE	2
17	SOUTH-WEST	2
18		3
19		3
20		4
TOTAL		30

ANSWER 18

Show ALL calculations.

APPLYING CORRECT FORMULA ✓

$$P = V1 + H + V2$$

$$= 150 + 80 + 150$$

$$= 380 \text{ m} / 380000 \text{ mm}$$

ANSWER ✓ / UNIT ✓

ANSWER 19

Show ALL calculations.


APPLYING CORRECT FORMULA ✓

$$\text{AREA} = (L \times B) - (L \times B)$$

$$= (65 \times 34) - (29 \times 9)$$

$$= 1949 \text{ m}^2$$

ANSWER 20

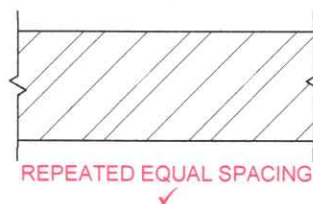
(a) SANS COMPLIANT ✓
(FACE BRICK)

(b)



SQUARE HOLE ✓

BOTH IN FREEHAND ●



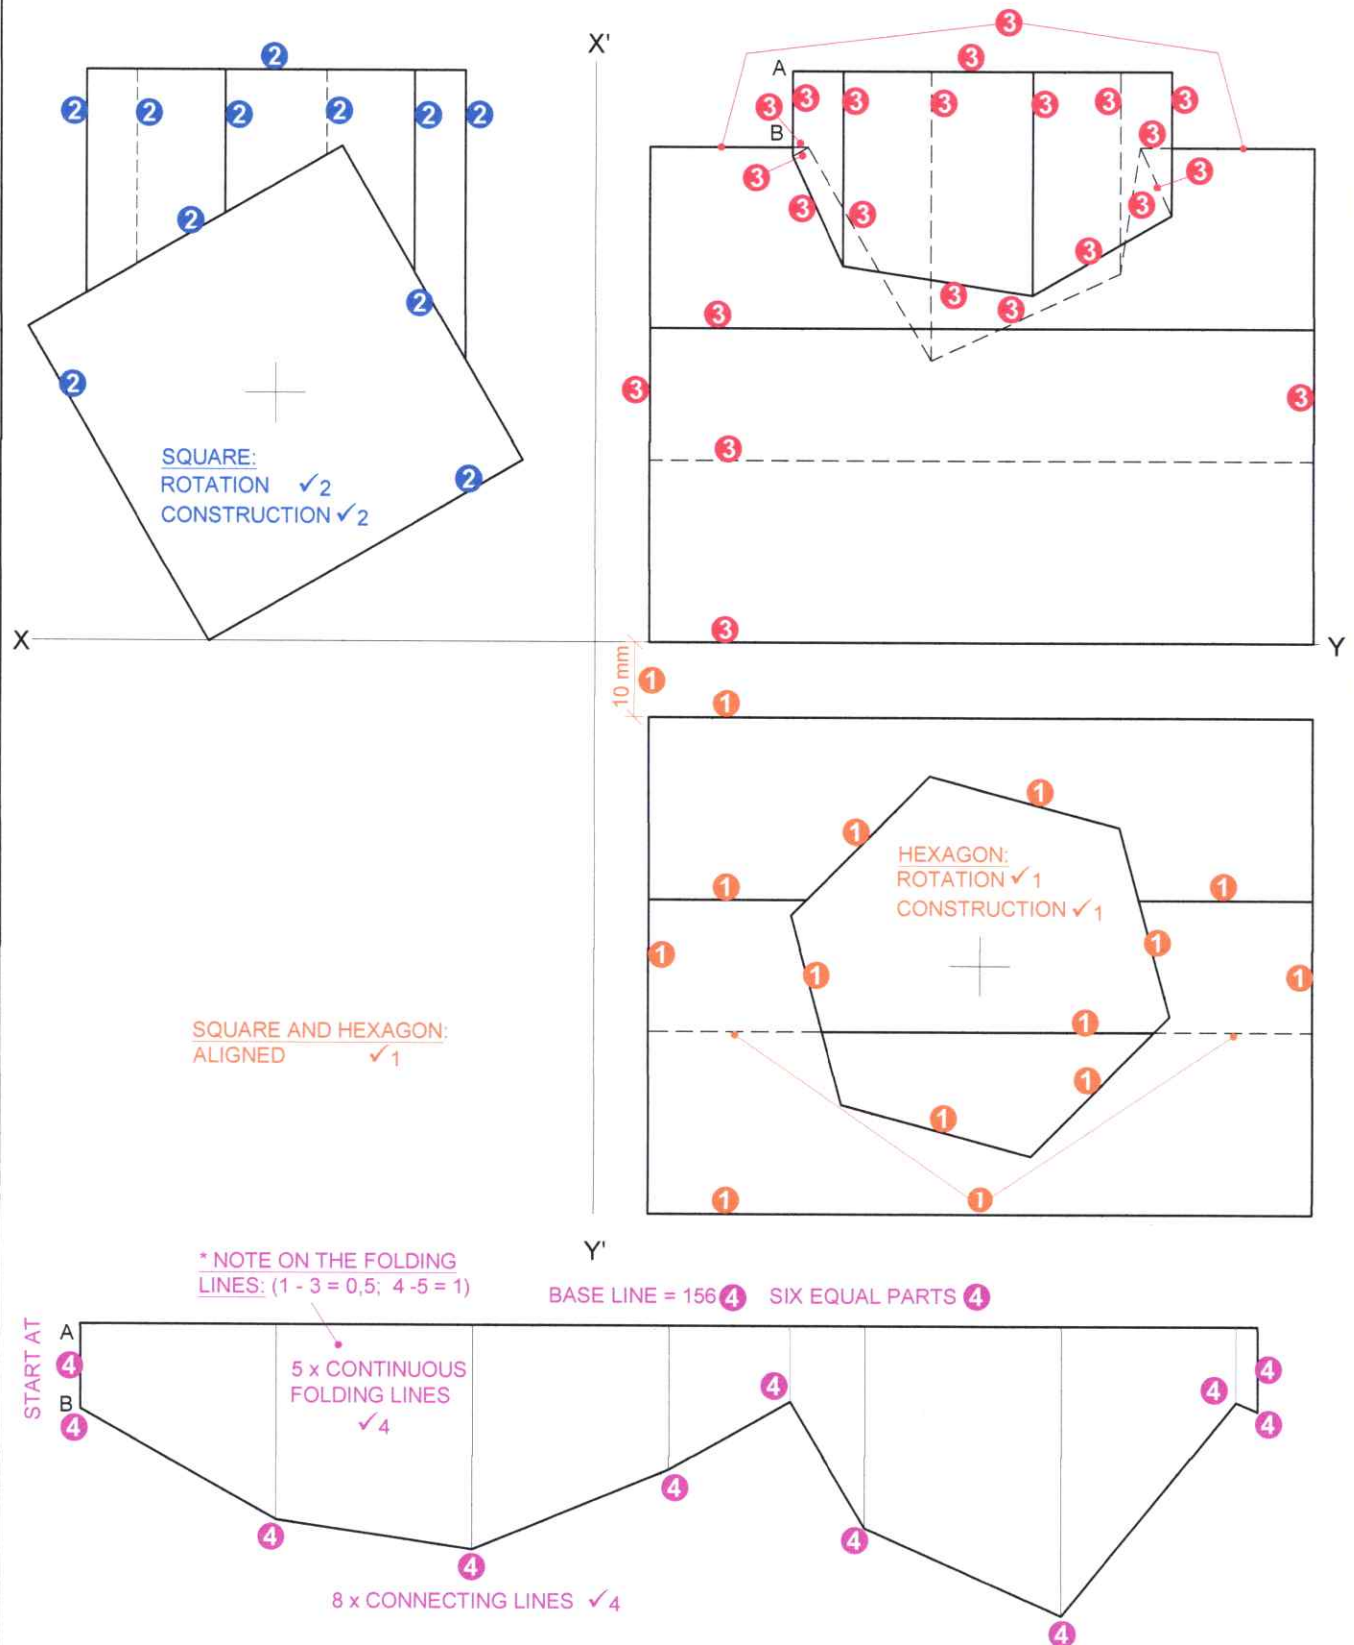


ASSESSMENT CRITERIA		
1	TOP VIEW	10 $\frac{1}{2}$
2	RIGHT VIEW	7 $\frac{1}{2}$
3	FRONT VIEW	11 $\frac{1}{2}$
4	DEVELOPMENT	8 $\frac{1}{2}$
TOTAL		38

PAPER 1 QUESTION 2
GRADE 12
DBE MAY/JUNE 2026
MARKING GUIDELINES




RVP

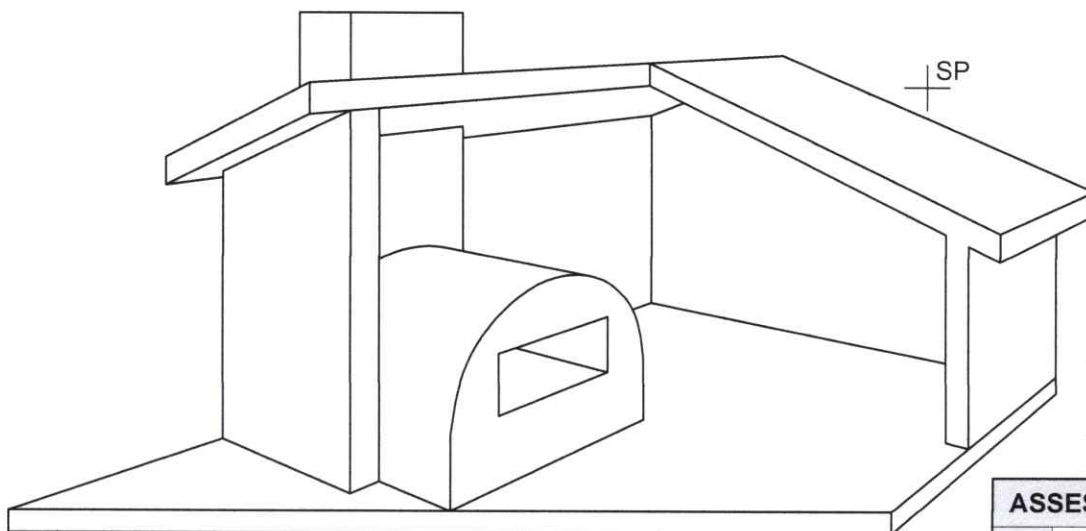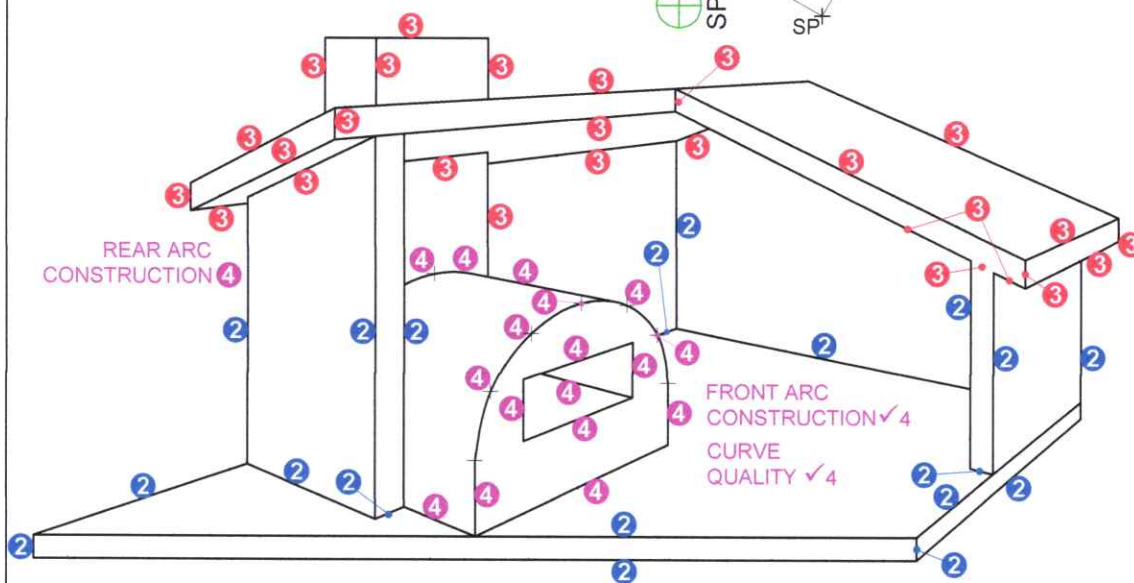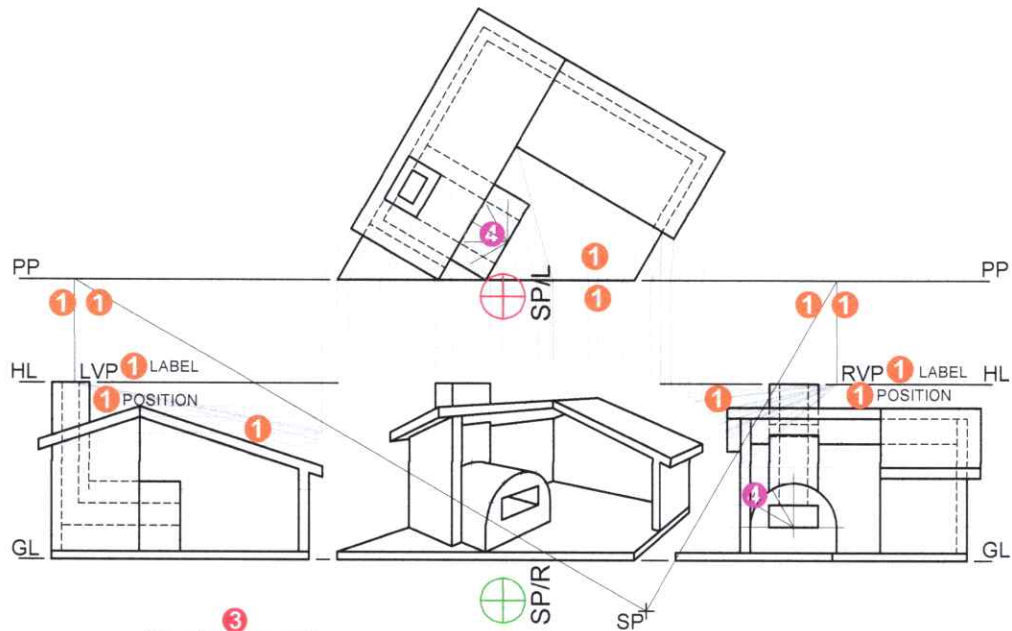

PAPER 1 QUESTION 3
GRADE 12
DBE MAY/JUNE 2026
MARKING GUIDELINES

ASSESSMENT CRITERIA		
1	CONSTRUCTION	6
2	FLOOR + WALLS	9½
3	ROOF + CHIMNEY	12½
4	OVEN	12
TOTAL		40

SP

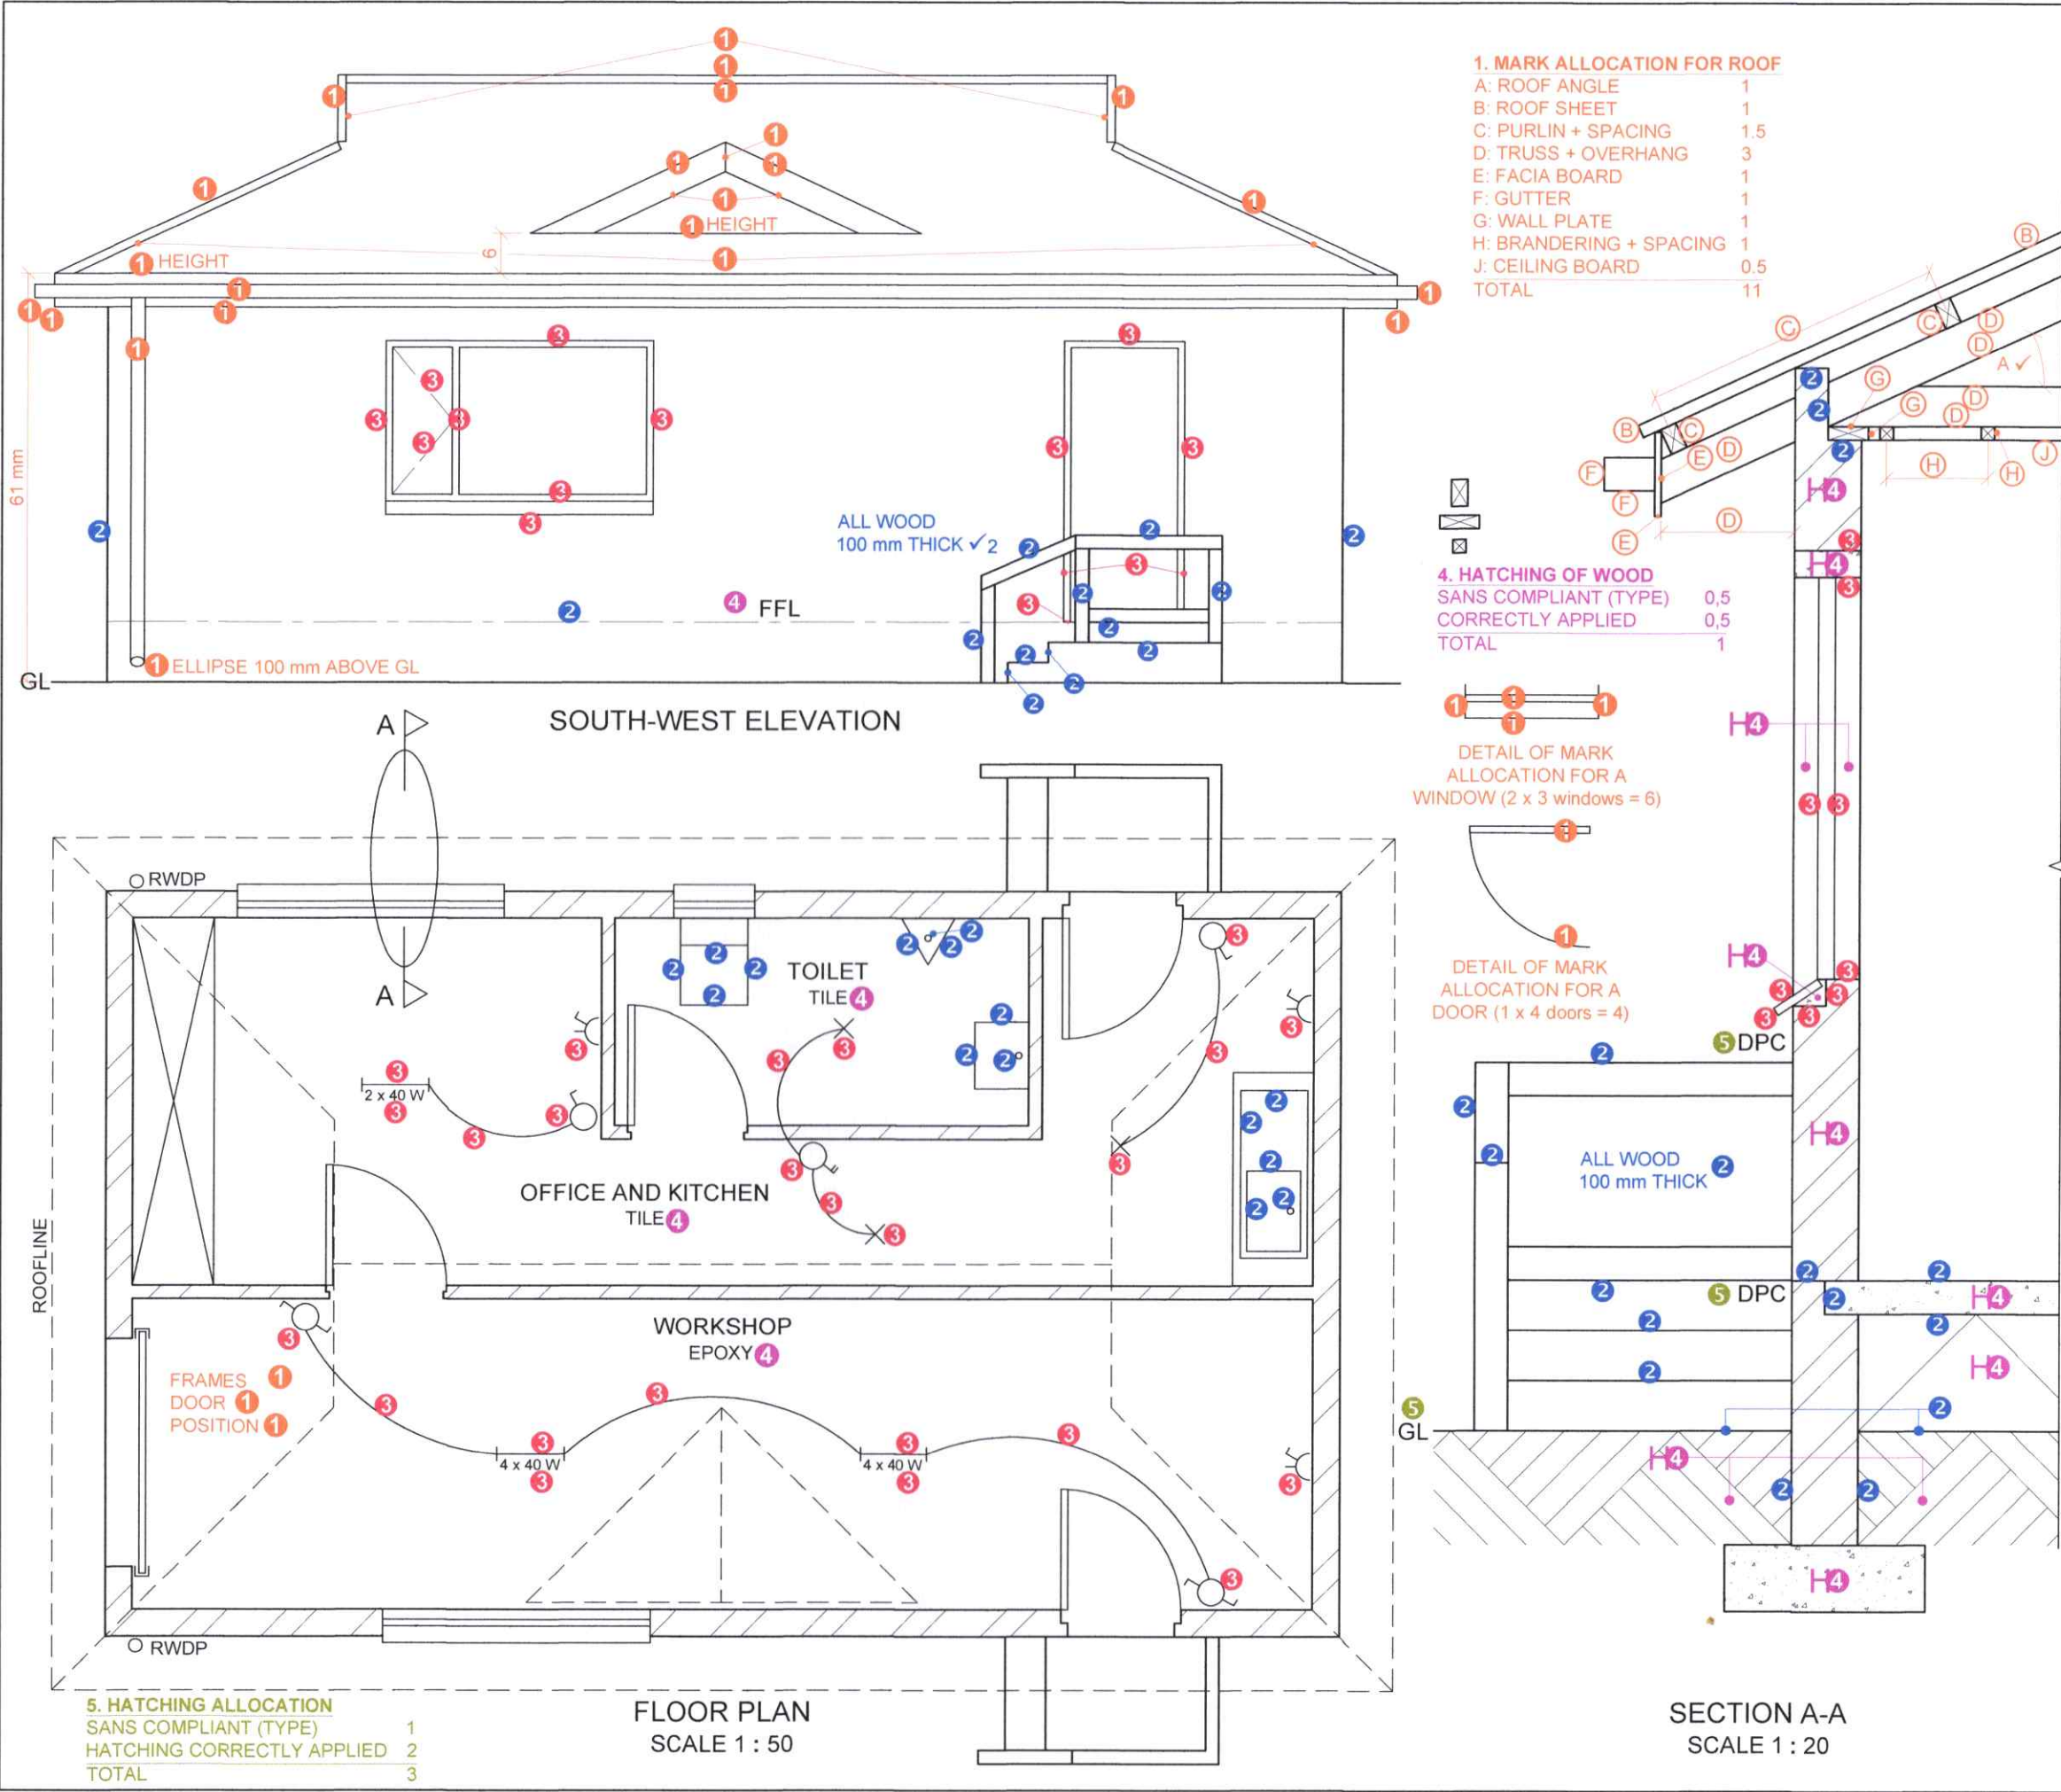

MARK ALLOCATION FOR SECTION OF ROOF		FOR OFFICIAL USE ONLY			
A		INCORRECT SCALE(S) USED			
B		NON-ALIGNMENT OF VIEWS			
C		VIEW(S) ROTATED			
D		SECTION VIEWED INCORRECTLY			
E		INCORRECT LETTERING			
F					
G					
H					
J					
TOTAL		TOTAL			

ASSESSMENT CRITERIA				
FLOOR PLAN				
		POSSIBLE	OBTAINED	SIGN MODERATED
1	DOORS + WINDOWS	11 1/2		
2	FIXTURES	7 1/2		
3	ELECTRICAL	12		
4	LABELS	1 1/2		
5	HATCHING	3		
SUBTOTAL		35 1/2		
SOUTH-WEST ELEVATION				
1	ROOF + RWDP	11		
2	WALLS + BALUSTRADE	7 1/2		
3	DOORS + WINDOWS	6 1/2		
4	LABELS	1/2		
SUBTOTAL		25 1/2		
DETAILED SECTION				
1	ROOF DETAIL	11		
2	SLAB + WALL	8 1/2		
3	WINDOW	4 1/2		
4	HATCHING	5 1/2		
5	LABELS	1 1/2		
SUBTOTAL		31		
TOTAL		92		
PENALTIES (-)				
GRAND TOTAL				